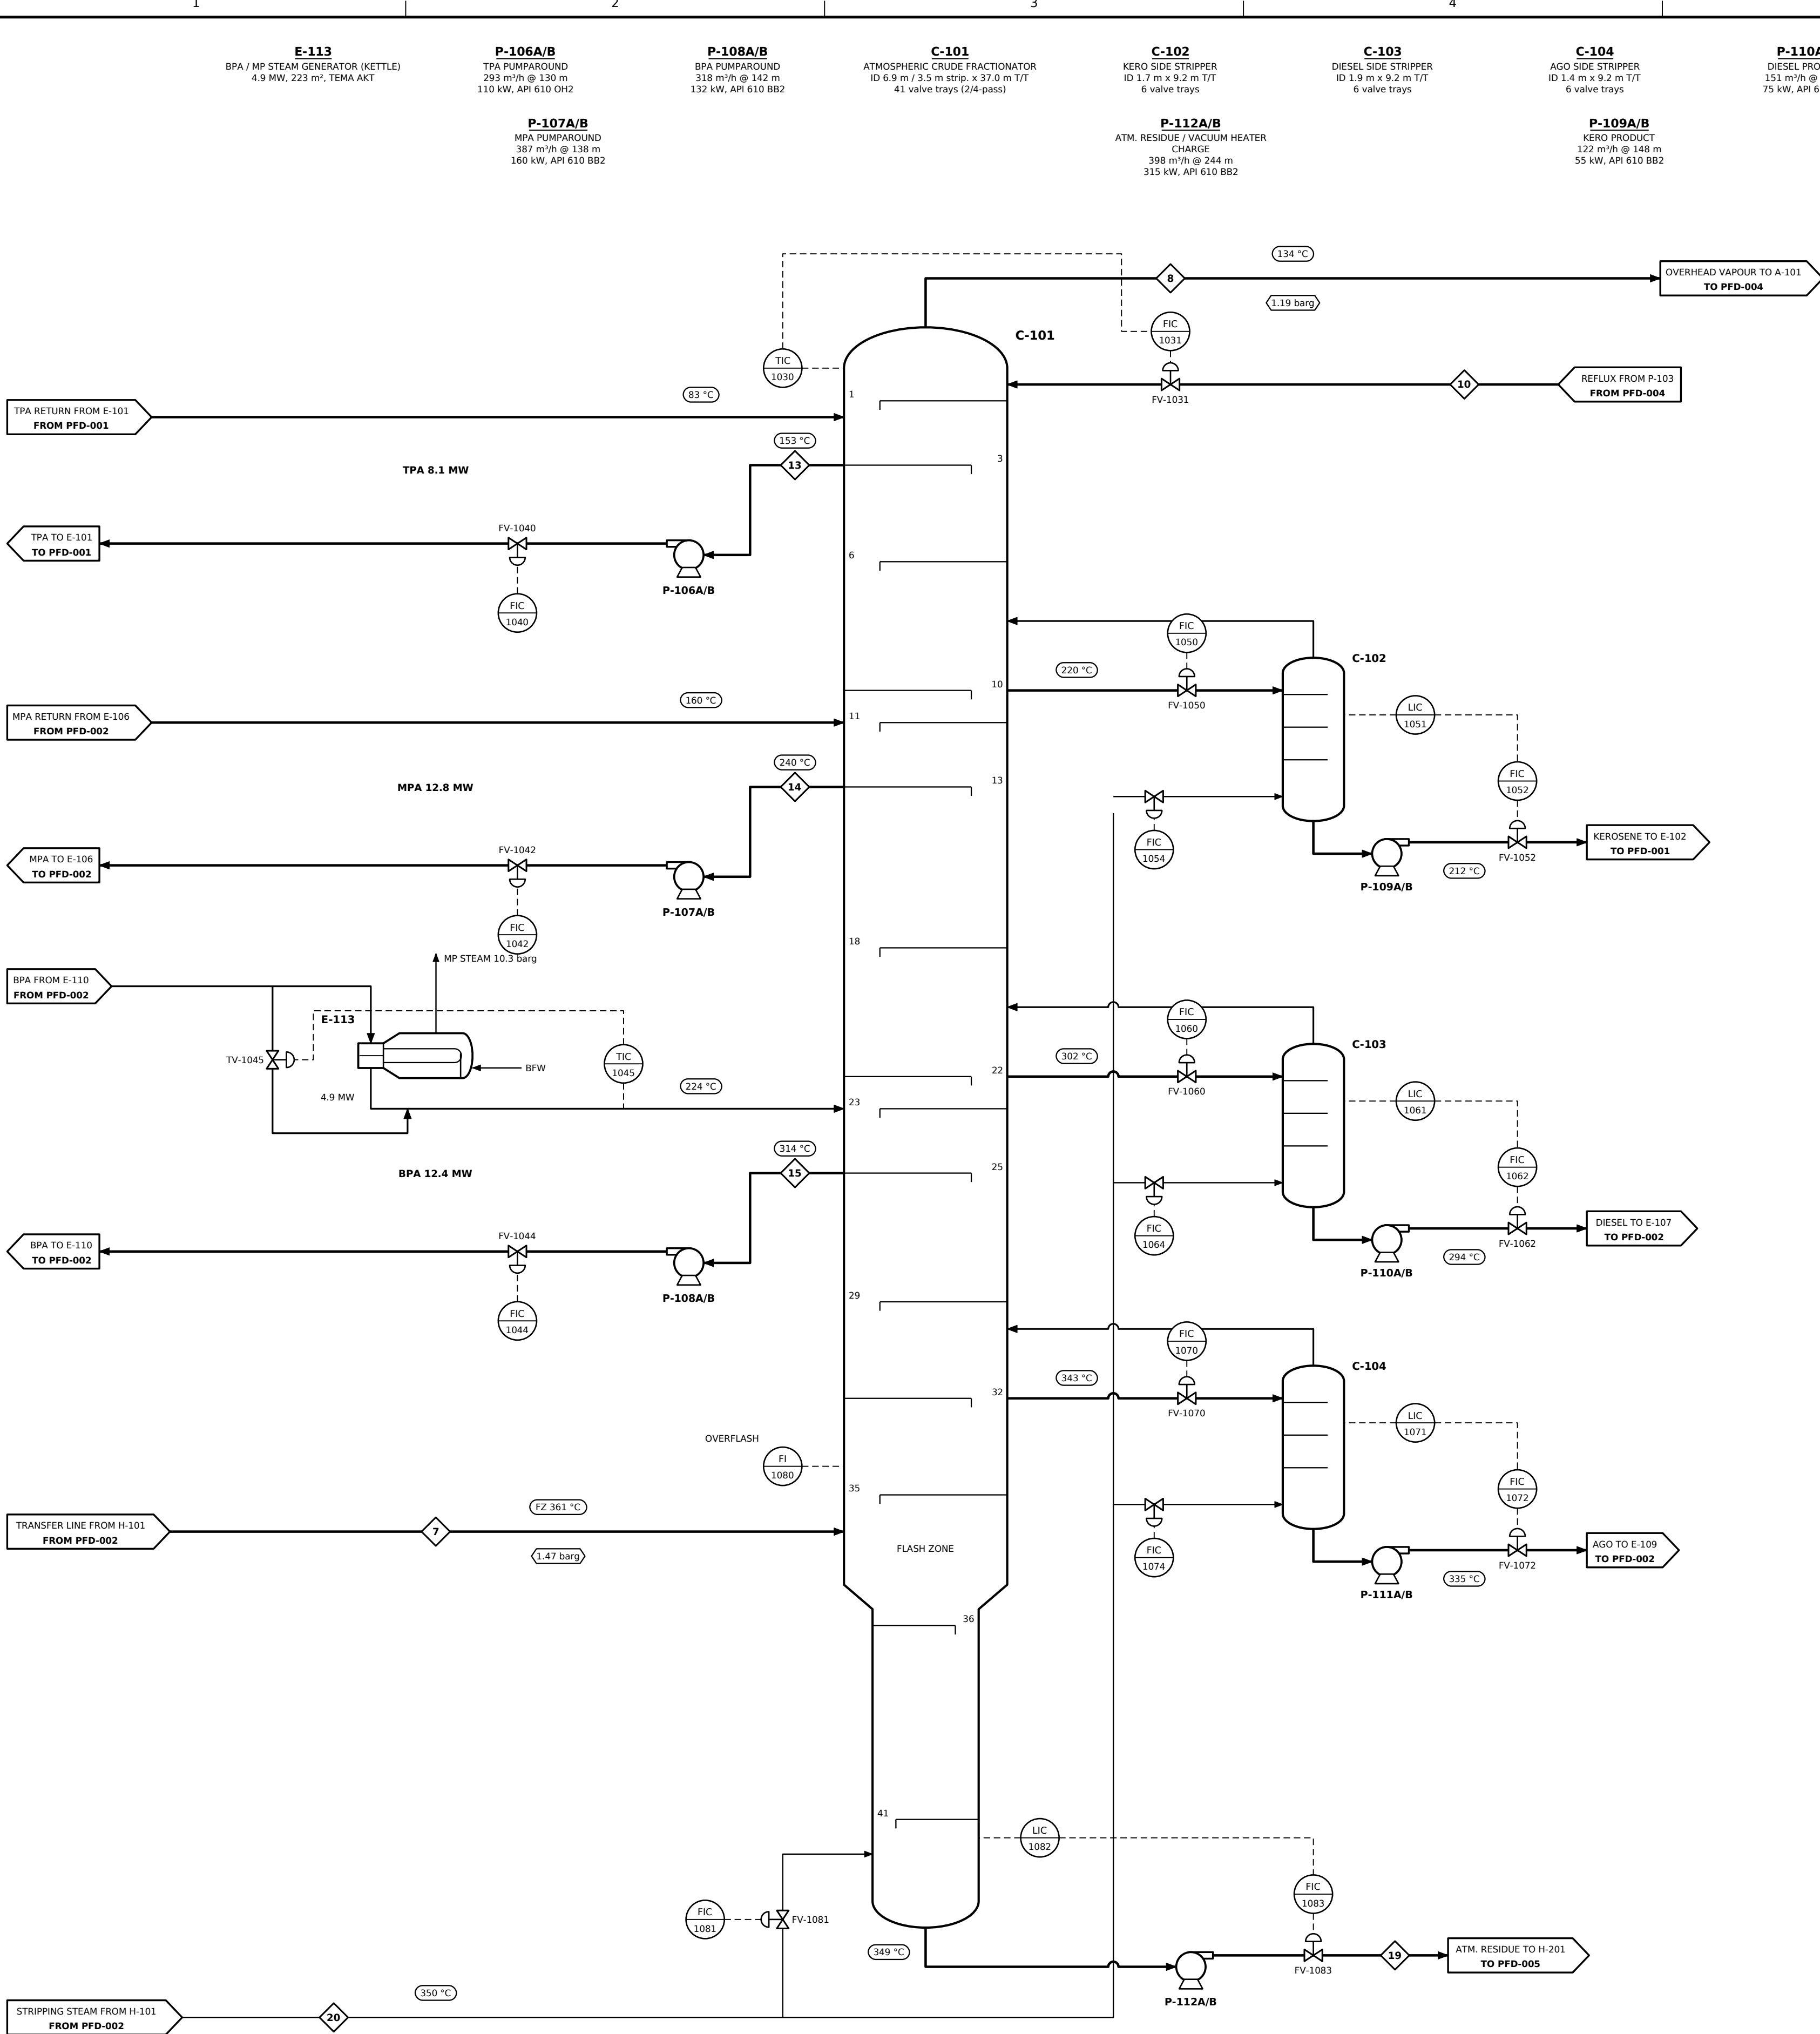


STREAM No.	②	⑥	⑩	⑬	⑭	⑮	⑯	⑰	⑱	⑲	⑳
DESCRIPTION	Heater outlet / transfer line	Column overhead vapour	Reflux	TPA pumparound (draw)	MPA pumparound (draw)	BPA pumparound (draw)	Kerosene product	Diesel product	AGO product	Atmospheric residue	Atm stripping steam (total)
PHASE	MIXED	VAPOUR	LIQUID	LIQUID	LIQUID	LIQUID	LIQUID	LIQUID	LIQUID	LIQUID	VAPOUR
TOTAL FLOW kg/h	569,197	229,224	101,310	166,764	208,349	165,727	68,595	81,613	45,847	256,909	11,681
TEMPERATURE °C	366	134	45	153	240	314	45	55	349	350	
PRESSURE barg	2.4	1.2	7.0	8.0	8.0	8.0	5.0	5.0	5.0	19.0	3.5
STD LIQ. FLOW BPSD	100,000	45,042	21,105	33,584	39,539	29,853	13,017	14,701	7,930	40,413	-
VAPOUR FRACTION (mass)	0.533	1	0	0	0	0	0	0	0	0	1
MOLECULAR WEIGHT	215.7	97.9	97.9	114.2	158.6	216.5	158.6	216.5	280.8	528.6	-

LEGEND

	H6MB STREAM No.		INSTRUMENT SIGNAL		MAIN PROCESS
	TEMPERATURE		CONTROL VALVE		SECONDARY PROCESS
	PRESSURE		SERVICE		UTILITY
	DCS CONTROLLER		TO PFD-00X OFF-SHEET CONNECTOR		FLUE GAS / AIR

NOTES

1. C-101 trays numbered top-down. Pumparound heat recovered in preheat trains (PFD-001/002).
2. Side-stripper draw rates (FIC-1050/1060/1070) set cut points; product rate on stripper level.
3. Stripping steam is LP steam superheated in H-1011 convection (stream 20).
4. Stream numbers (diamonds) refer to H6MB CFU-000-PR-HMB-001; data from design case, normal operation.
5. Pressures bar(g) unless noted. Pumps A/B are 2 x 100 %; only duty pump shown.

REV	DATE	DESCRIPTION	
A	2026-10-02	Issued for review (FEED)	
GENERIC REFINERY - GULF COAST 100 KBPSD CRUDE & VACUUM DISTILLATION UNIT			
PROCESS FLOW DIAGRAM ATMOSPHERIC COLUMN C-101, PUMPAROUNDS & SIDE STRIPPERS			
DISCIPLINE	STAGE	SCALE	SHEET
PROCESS	FEED	NTS	3 OF 6
DRAWN	CHECKED	APPROVED	DATE
CLAUDE CODE	-	-	2026-10-02
DRAWING NUMBER			REV
CFU-100-PR-PFD-003			A