


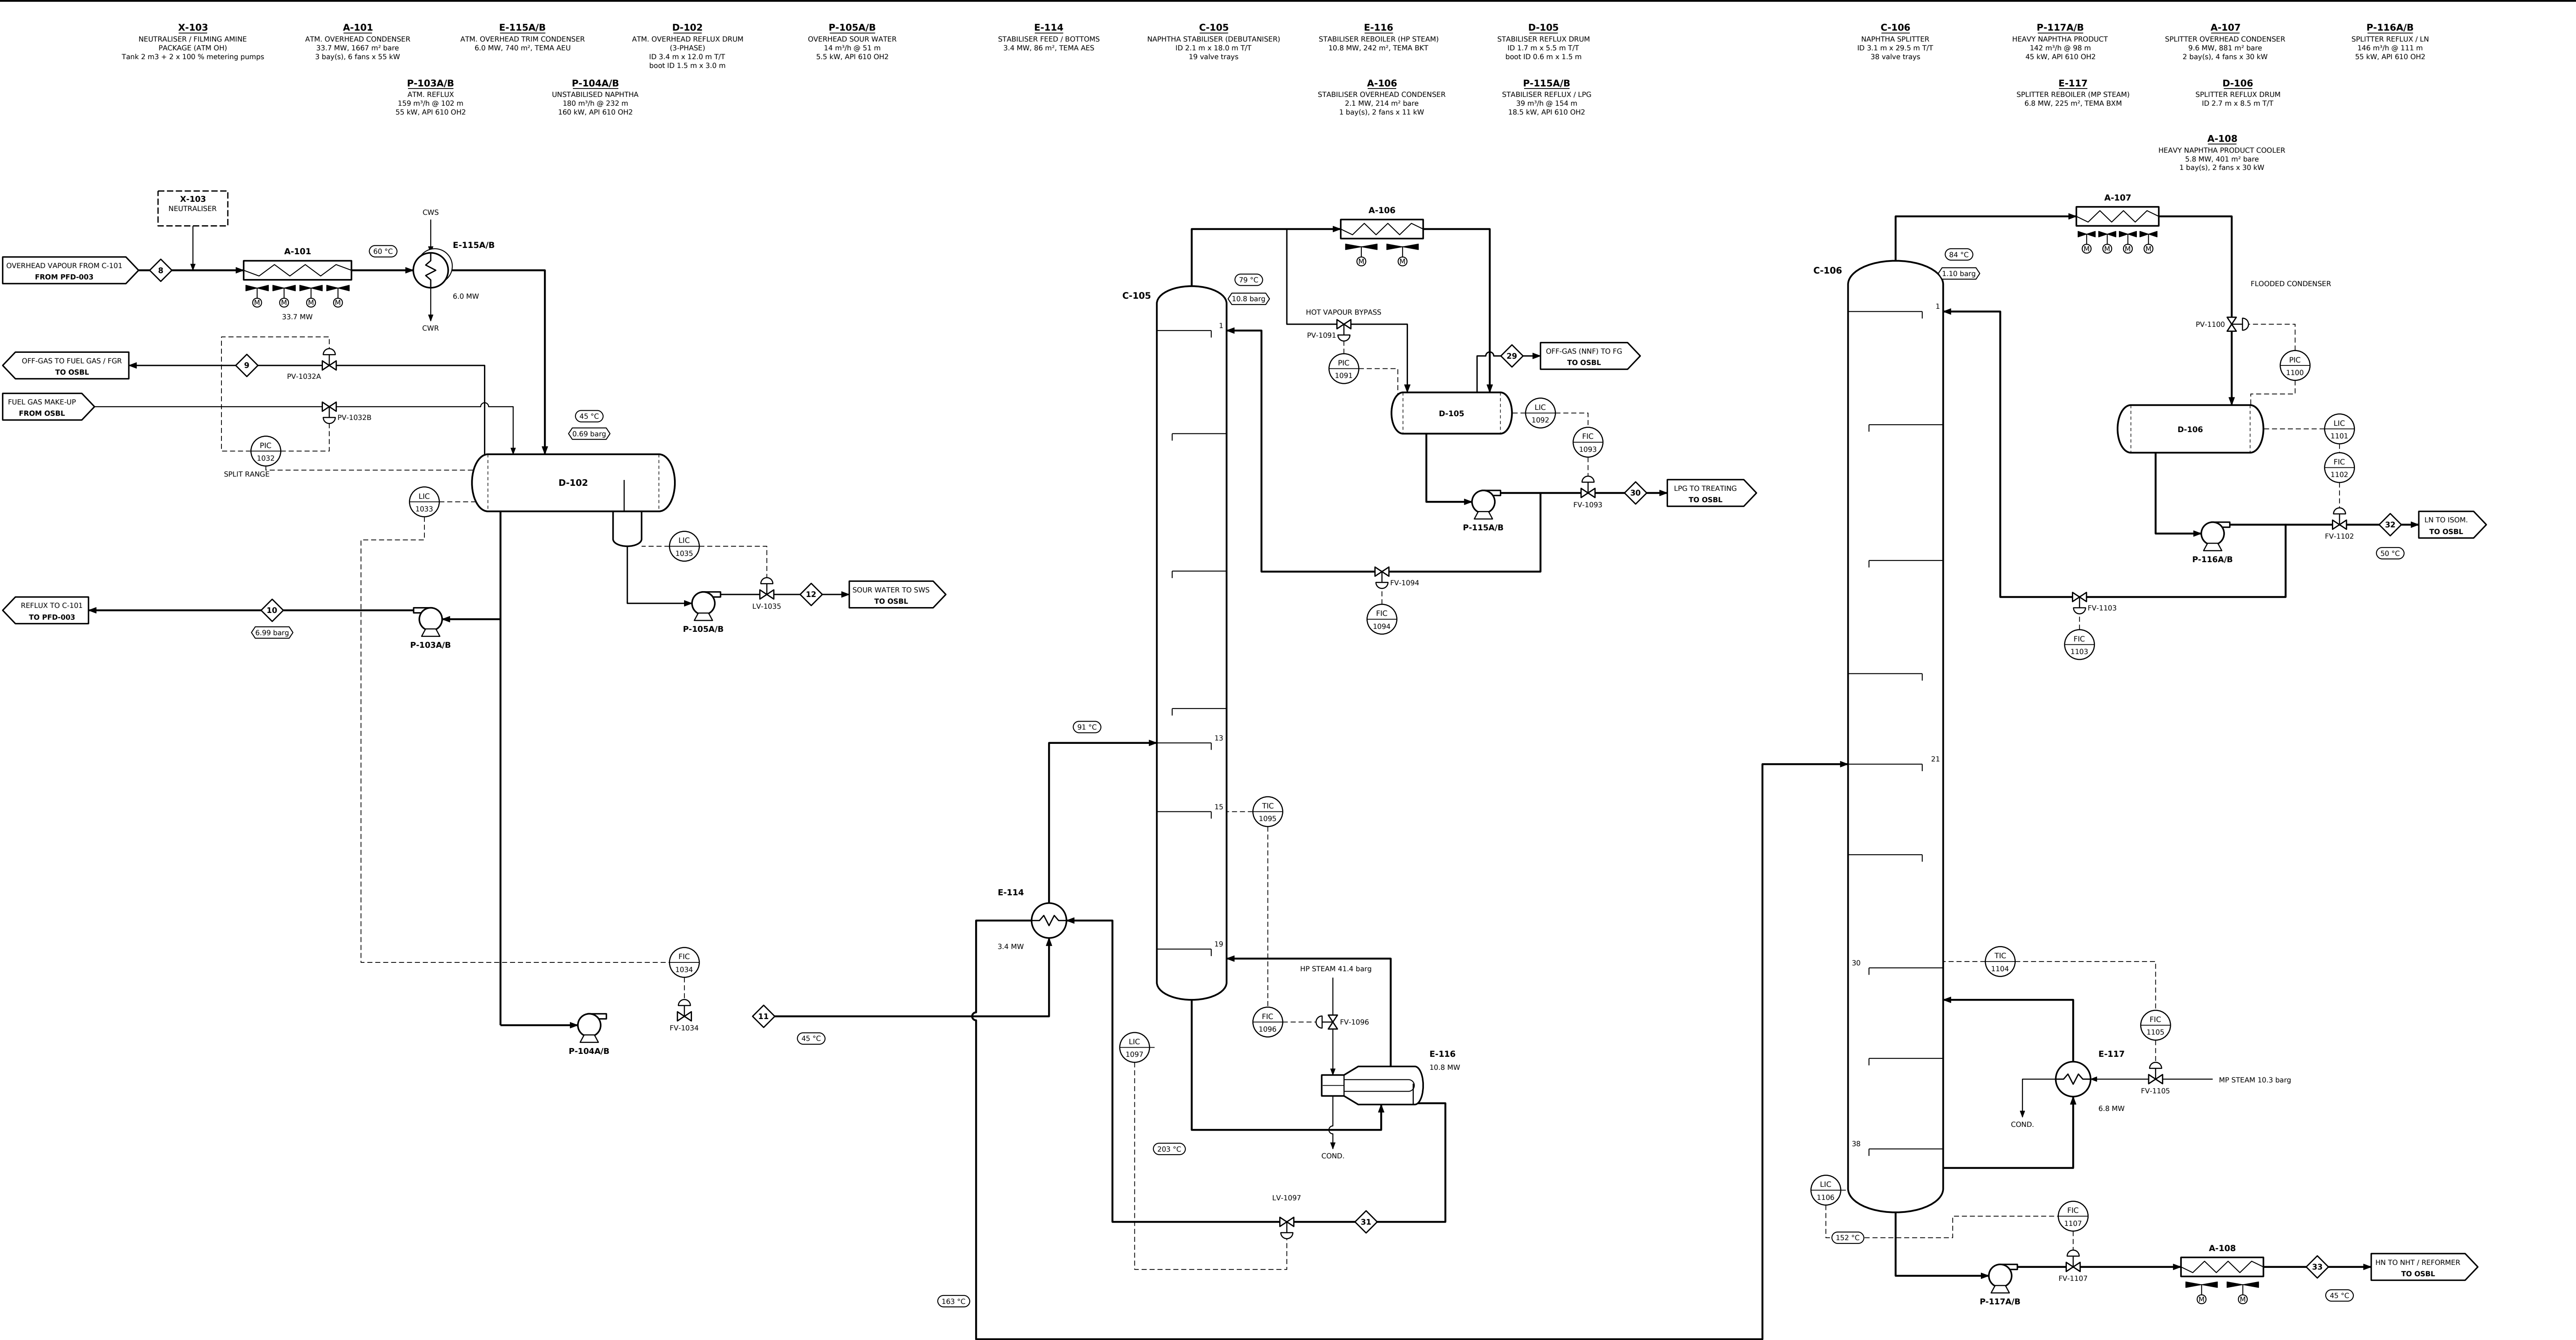

STREAM No.	0	9	10	11	12	25	30	32	42	32
DESCRIPTION	Column overhead vapour	Overhead drum off-gas (NNF)	Reflux	Unstabilised naphtha	Overhead sour water	Stabiliser off-gas (NNF)	LPG product	Stabilised naphtha	Light naphtha	Heavy naphtha
PHASE	VAPOUR	VAPOUR	LIQUID	LIQUID	WATER	VAPOUR	LIQUID	LIQUID	LIQUID	LIQUID
TOTAL FLOW kg/h	229,224	0	101,310	114,910	13,004	0	6,468	108,442	27,607	80,835
TEMPERATURE °C	134	45	45	45	45	45	203	50	45	45
PRESSURE barg	1.2	0.7	7.0	14.0	5.0	10.5	17.0	11.3	7.0	7.0
STD LIQ. FLOW BPSD	45,042	-	21,105	23,938	-	-	1,743	22,195	5,920	16,275
VAPOUR FRACTION (mass)	1	-	0	0	-	-	0	0	0	0
MOLECULAR WEIGHT	97.9	-	97.9	97.9	-	-	54.2	102.9	81.0	113.3

00

H&MB STREAM No.

000 °C

TEMPERATURE

0.0 barg

PRESSURE

FIC 1034

DCS CONTROLLER

INSTRUMENT SIGNAL

CONTROL VALVE

SERVICE CONNECTOR

TO PFD-00X

MAIN PROCESS

SECONDARY PROCESS

UTILITY

FLUE GAS / AIR

NOTES

1. D-102 pressure by split range; PV-1032A off-gas to FG/FG, PV-1032B fuel gas make-up.
2. C-105 pressure by hot-vapour bypass PV-1091; C-106 by flooded condenser PV-1100.
3. Reboiler duties set by sensitive-tray temperature cascades (TIC-1095, TIC-1104).
4. Stream numbers (diamonds) refer to H&MB CFU-000-PR-HMB-001; data from design case, normal operation.
5. Pressures bar(g) unless noted. Pumps A/B are 2 x 100 %; only duty pump shown.

REV	DATE	DESCRIPTION
A	2026-10-02	Issued for review (FEED)
GENERIC REFINERY - GULF COAST		
100 KBPSD CRUDE & VACUUM DISTILLATION UNIT		
PROCESS FLOW DIAGRAM		
ATMOSPHERIC OVERHEAD SYSTEM, STABILISER & NAPHTHA SPLITTER		
DISCIPLINE	STAGE	SCALE
PROCESS	FEED	NTS
CLAUDE CODE	CHECKED	APPROVED
DRAWING NUMBER	DATE	REV
CFU-100-PR-PFD-004		A