


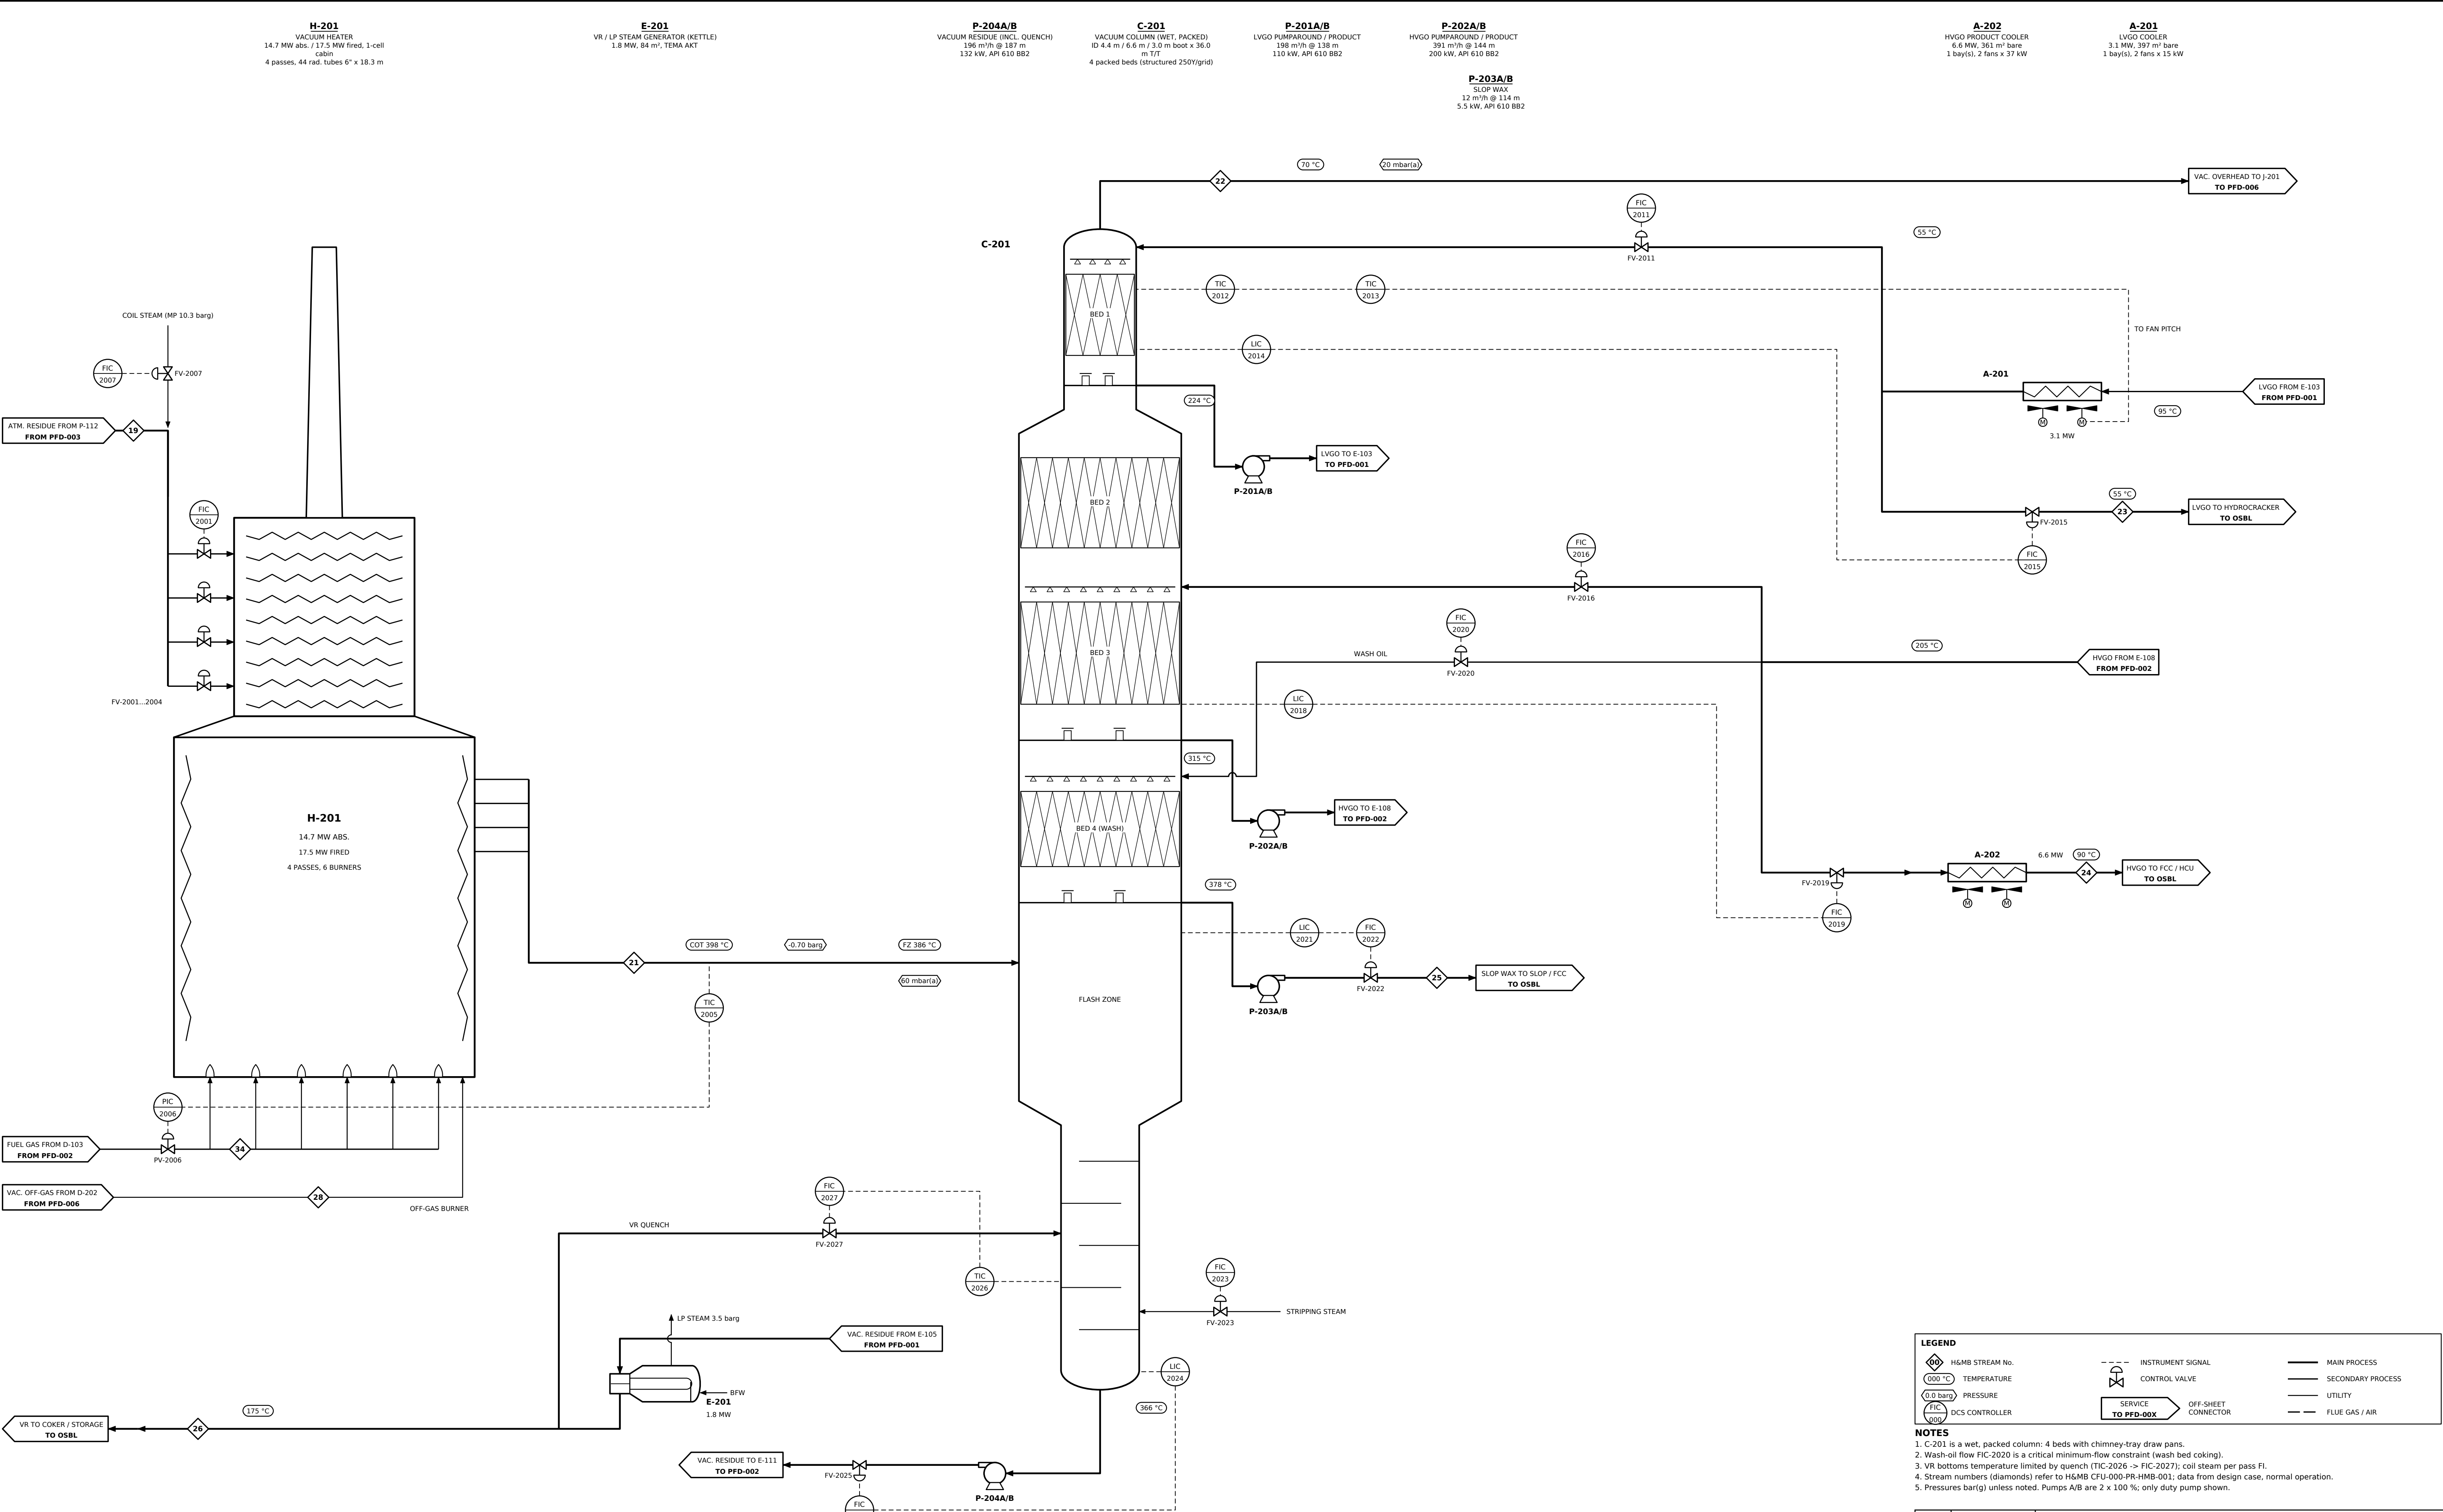

STREAM No.	19	21	22	23	24	25	26	27	28
DESCRIPTION	Atmospheric residue	Vacuum heater outlet	Vacuum column overhead	LVGO product	HVGO product	Slop wax	Vacuum residue	Vacuum off-gas (NCG + air)	Fuel gas to heaters
PHASE	LIQUID	MIXED	VAPOUR	LIQUID	LIQUID	LIQUID	LIQUID	VAPOUR	VAPOUR
TOTAL FLOW kg/h	256,909	258,055	3,020	50,356	90,396	7,894	108,263	102	6,504
TEMPERATURE °C	349	398	70	55	90	175	45	30	30
PRESSURE barg	19.0	-0.70	-0.99	7.0	7.0	9.0	0.0	3.5	3.5
STD LIQ. FLOW BPSD	40,413	40,413	-	8,467	14,553	1,212	16,181	-	-
VAPOUR FRACTION (mass)	0	0.264	1	0	0	0	0	1	1
MOLECULAR WEIGHT	528.6	528.6	-	339.7	462.4	671.3	829.6	-	-

REV	DATE	DESCRIPTION
A	2026-10-02	Issued for review (FEED)
GENERIC REFINERY - GULF COAST		
100 KBPSD CRUDE & VACUUM DISTILLATION UNIT		
PROCESS FLOW DIAGRAM		
VACUUM HEATER H-201 & VACUUM COLUMN C-201		
DISCIPLINE	STAGE	SCALE
PROCESS	FEED	NTS
DRAWN	CHECKED	APPROVED
CLAUDE CODE	-	-
DRAWING NUMBER	CFU-200-PR-PFD-005	
DATE	2026-10-02	REV
5 OF 6		A