


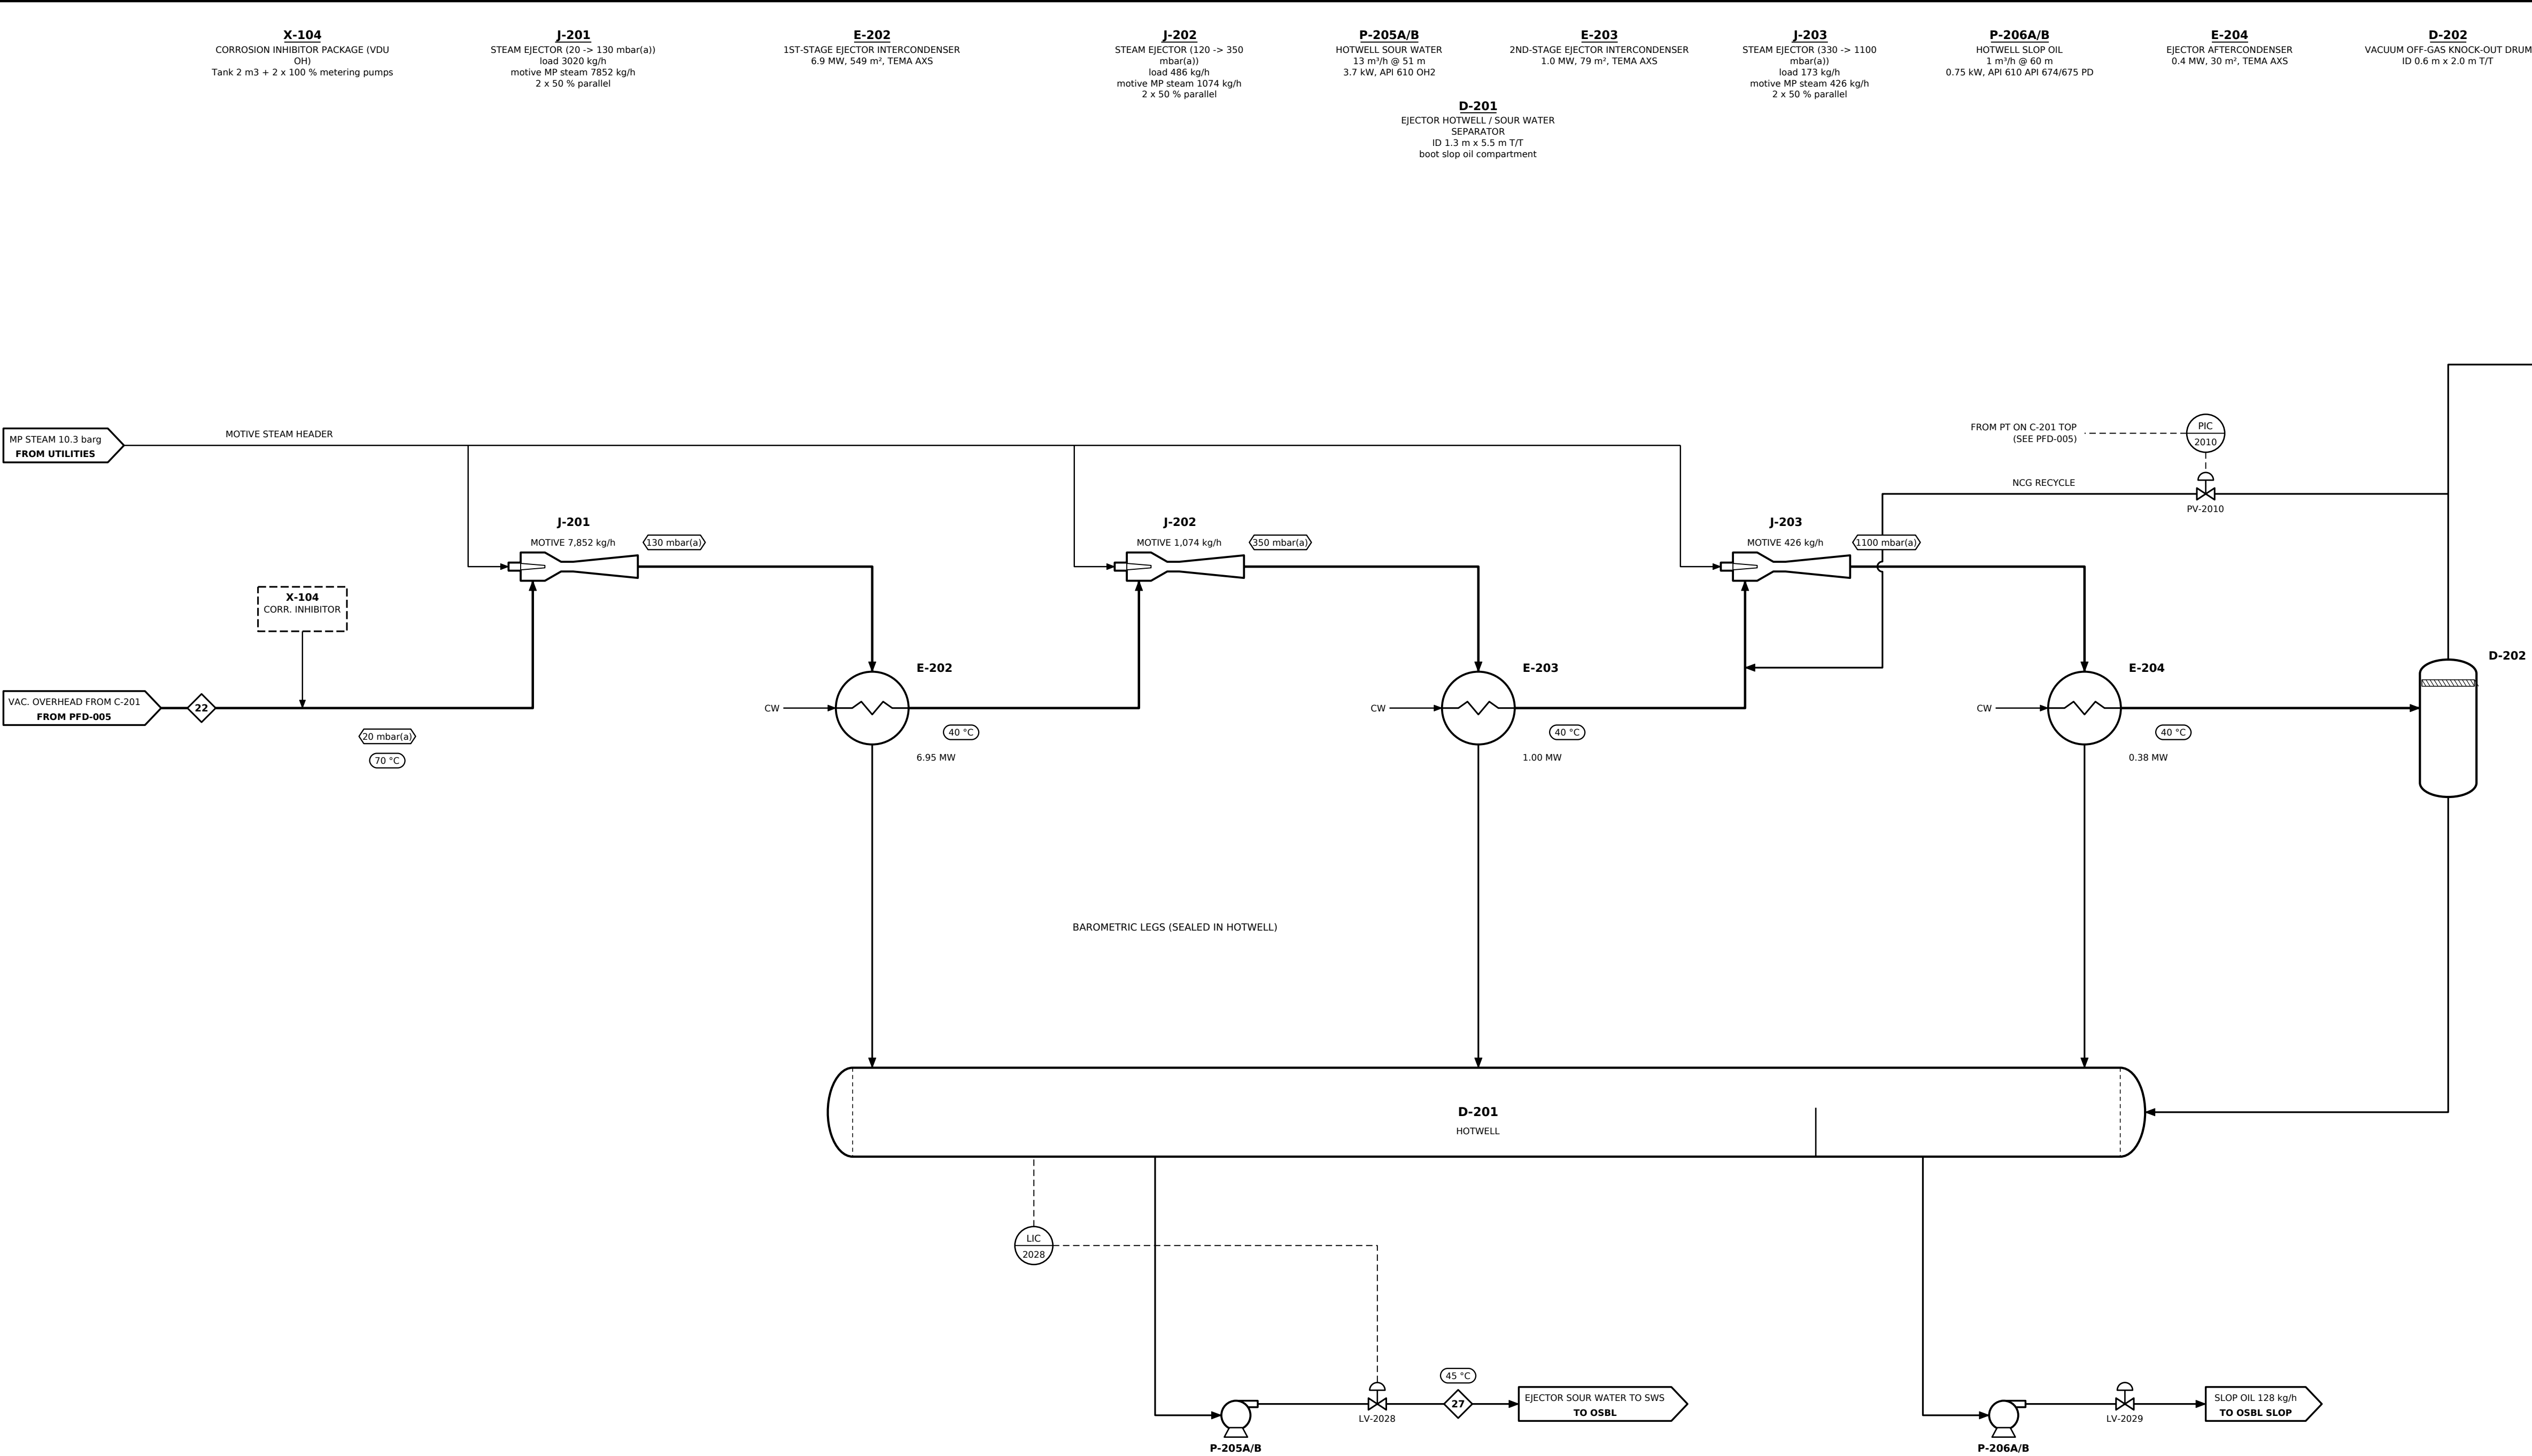

STREAM No.	22	27	28
DESCRIPTION	Vacuum column overhead	Ejector sour water	Vacuum off-gas (NCG + air)
PHASE	VAPOUR	WATER	VAPOUR
TOTAL FLOW kg/h	3,020	12,141	102
TEMPERATURE °C	70	45	45
PRESSURE barg	-0.99	0.5	0.0
STD LIQ. FLOW BPSD	-	-	-
VAPOUR FRACTION (mass)	1	-	1
MOLECULAR WEIGHT	-	-	-

H&MB STREAM No.

TEMPERATURE

PRESSURE

DCS CONTROLLER

INSTRUMENT SIGNAL

CONTROL VALVE

SERVICE TO PFD-00X

MAIN PROCESS

SECONDARY PROCESS

UTILITY

FLUE GAS / AIR

- NOTES**
- Each ejector stage 2 x 50 % parallel units; one shown. Motive MP steam.
 - Condensers E-202/203/204 drain via barometric legs (seal) to hotwell D-201.
 - C-201 top pressure PIC-2010 (transmitter on C-201 top, PFD-005) recycles off-gas to J-203 suction.
 - Stream numbers (diamonds) refer to H&MB CFU-000-PR-HMB-001; data from design case, normal operation.
 - Pressures bar(g) unless noted. Pumps A/B are 2 x 100 %; only duty pump shown.

REV	DATE	DESCRIPTION	
A	2026-10-02	Issued for review (FEED)	
GENERIC REFINERY - GULF COAST 100 KBPSD CRUDE & VACUUM DISTILLATION UNIT			
PROCESS FLOW DIAGRAM VACUUM EJECTOR SYSTEM & HOTWELL			
DISCIPLINE	STAGE	SCALE	SHEET
PROCESS	FEED	NTS	6 OF 6
DRAWN	CHECKED	APPROVED	DATE
CLAUDE CODE	-	-	2026-10-02
DRAWING NUMBER			REV
CFU-200-PR-PFD-006			A