


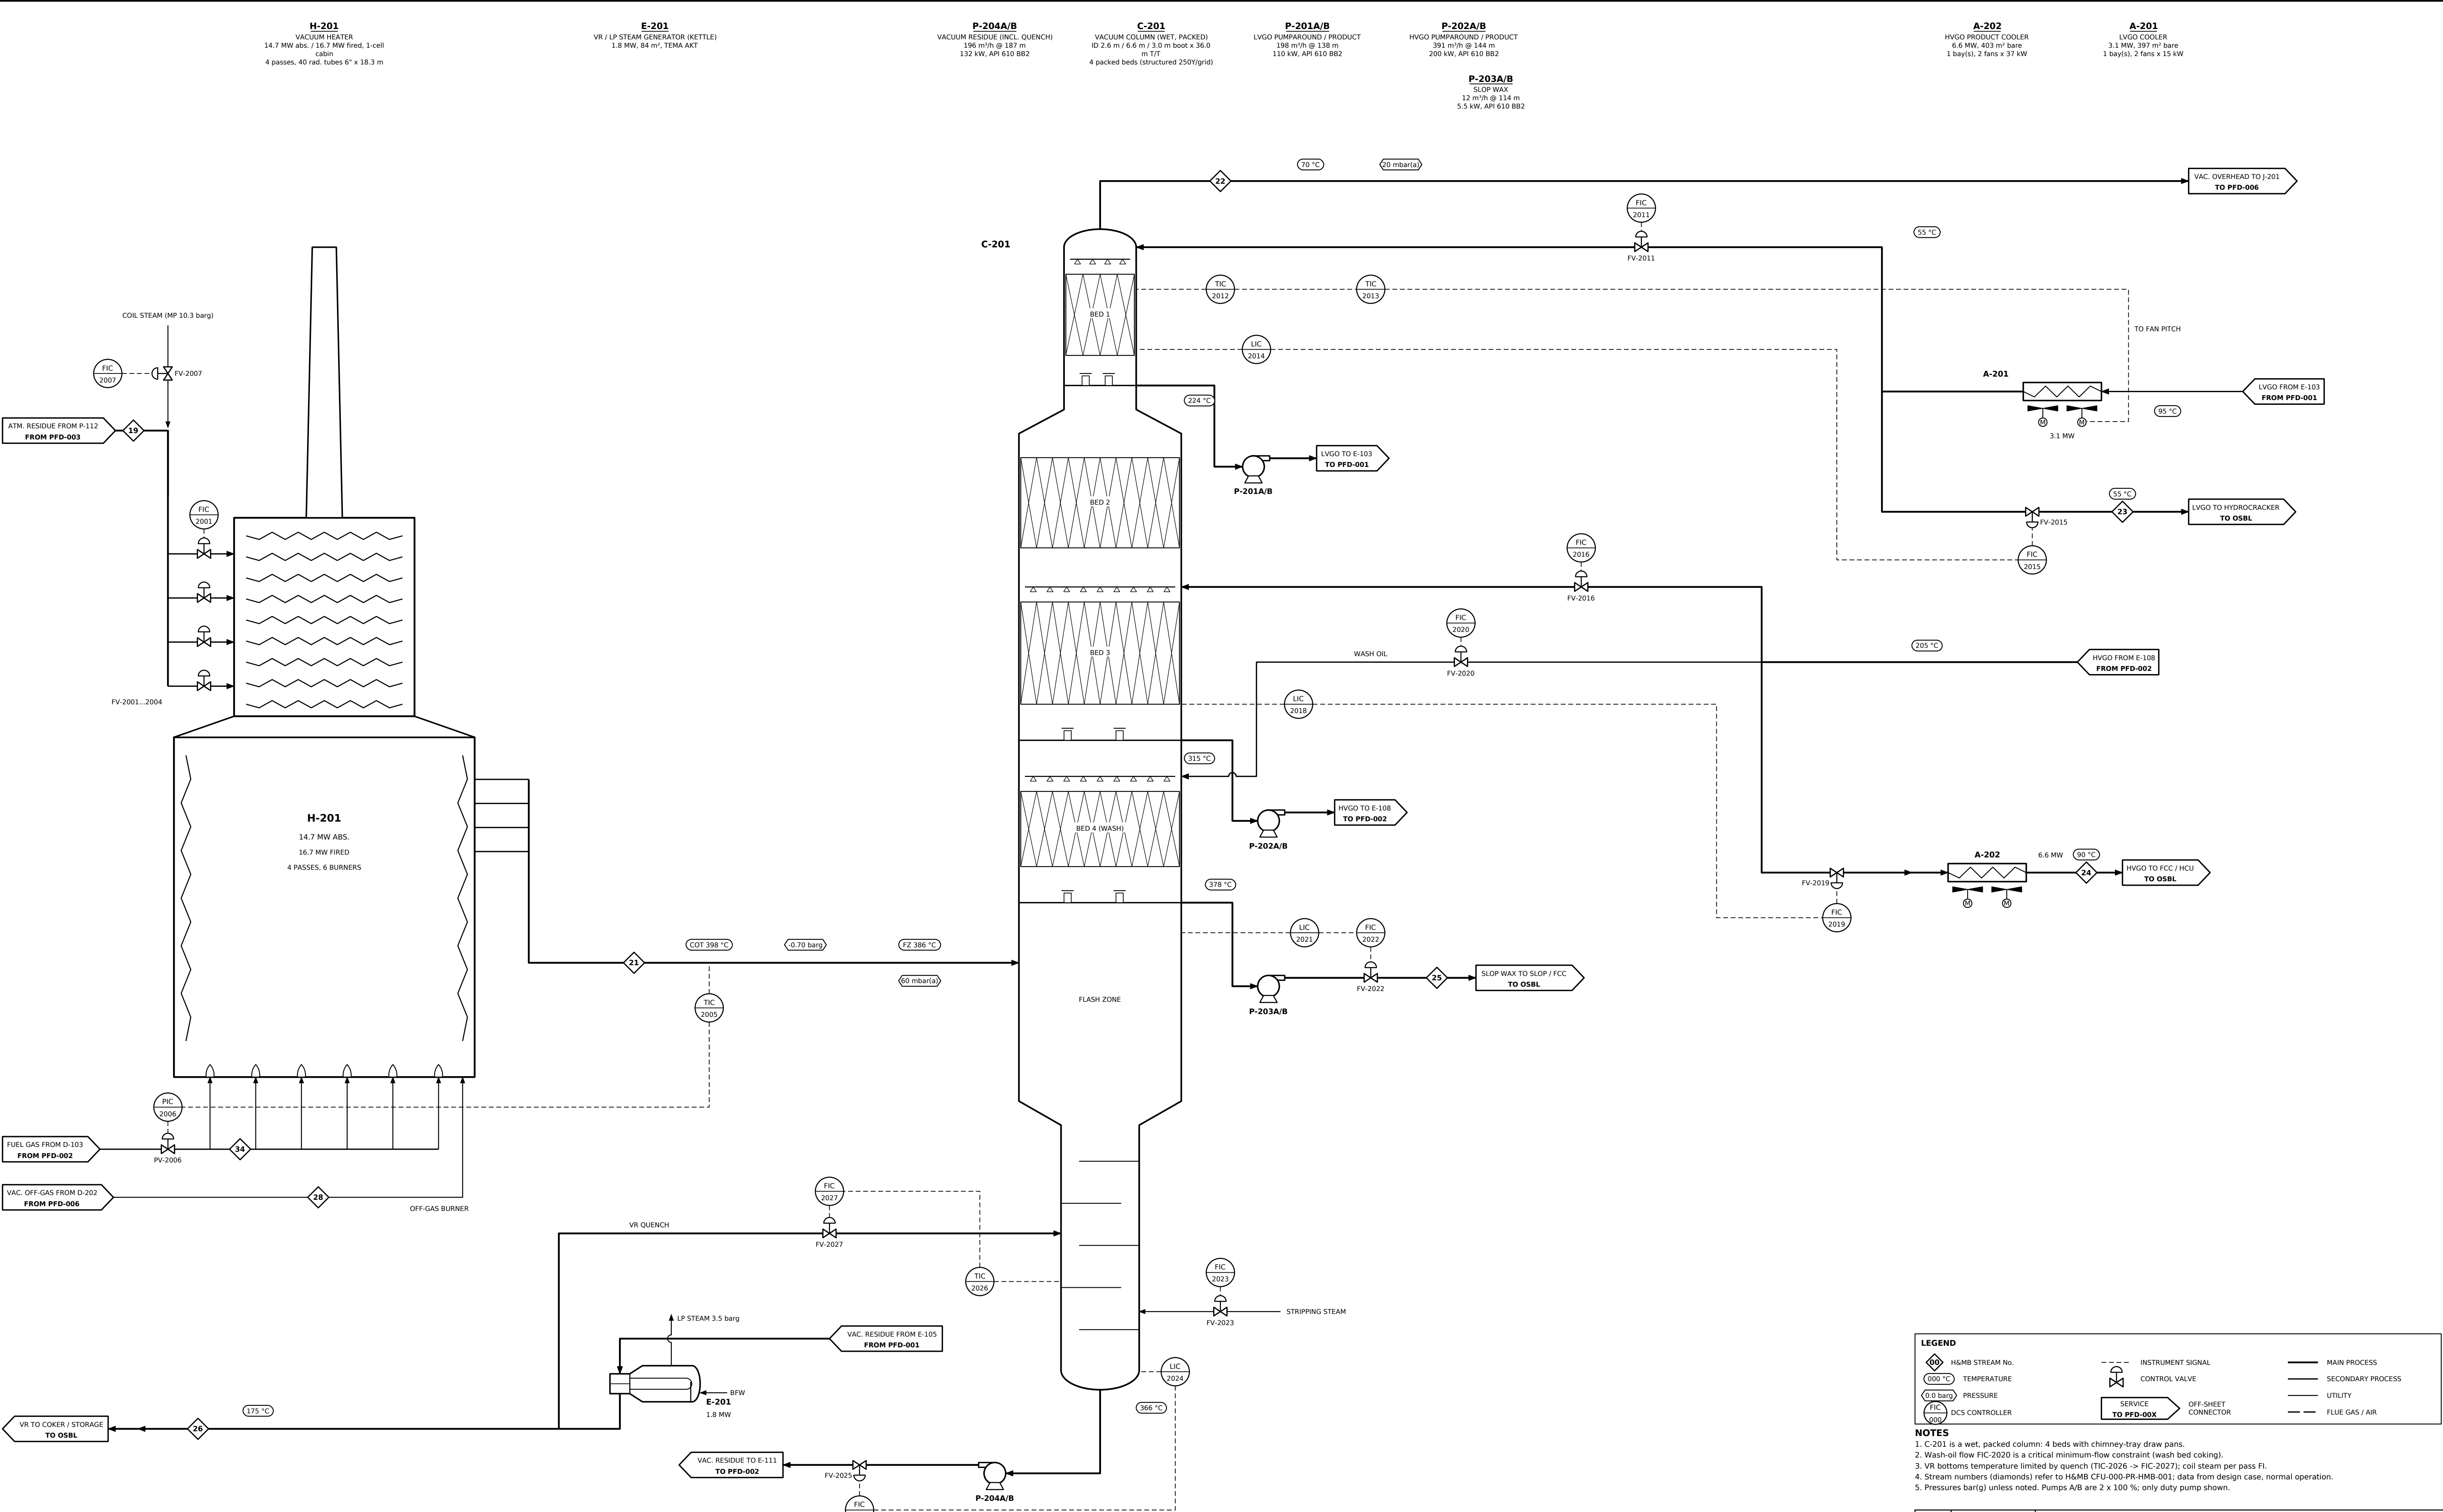

STREAM No.	19	21	22	23	24	25	26	27	28
DESCRIPTION	Atmospheric residue	Vacuum heater outlet	Vacuum column overhead	LVGO product	HVGO product	Slop wax	Vacuum residue	Vacuum off-gas (NCG + air)	Fuel gas to heaters
PHASE	LIQUID	MIXED	VAPOUR	LIQUID	LIQUID	LIQUID	LIQUID	VAPOUR	VAPOUR
TOTAL FLOW kg/h	256,909	258,055	3,020	50,356	90,396	7,894	108,263	102	6,443
TEMPERATURE °C	349	398	70	55	90	175	45	30	30
PRESSURE barg	19.0	-0.70	-0.99	7.0	7.0	9.0	0.0	3.5	-
STD LIQ. FLOW BPSD	40,413	40,413	-	8,467	14,553	1,212	16,181	-	-
VAPOUR FRACTION (mass)	0	0.264	1	0	0	0	1	1	-
MOLECULAR WEIGHT	528.6	528.6	-	339.7	462.4	671.3	829.6	-	-

H&MB STREAM No.

TEMPERATURE

PRESSURE

DCS CONTROLLER

INSTRUMENT SIGNAL

CONTROL VALVE

SERVICE TO PFD-00X

MAIN PROCESS

SECONDARY PROCESS

UTILITY

FLUE GAS / AIR

- NOTES**
- C-201 is a wet, packed column: 4 beds with chimney-tray draw pans.
 - Wash-oil flow FIC-2020 is a critical minimum-flow constraint (wash bed coking).
 - VR bottoms temperature limited by quench (TIC-2026 -> FIC-2027); coil steam per pass FI.
 - Stream numbers (diamonds) refer to H&MB CFU-000-PR-HMB-001; data from design case, normal operation.
 - Pressures bar(g) unless noted. Pumps A/B are 2 x 100 %; only duty pump shown.

REV	DATE	DESCRIPTION
A	2026-10-02	Issued for review (FEED)
GENERIC REFINERY - GULF COAST		
100 KBPSD CRUDE & VACUUM DISTILLATION UNIT		
PROCESS FLOW DIAGRAM		
VACUUM HEATER H-201 & VACUUM COLUMN C-201		
DISCIPLINE	STAGE	SCALE
PROCESS	FEED	NTS
5 OF 6		SHEET
DRAWN	CHECKED	APPROVED
CLAUDE CODE	-	-
DATE	2026-10-02	REV
DRAWING NUMBER	CFU-200-PR-PFD-005	
A		