


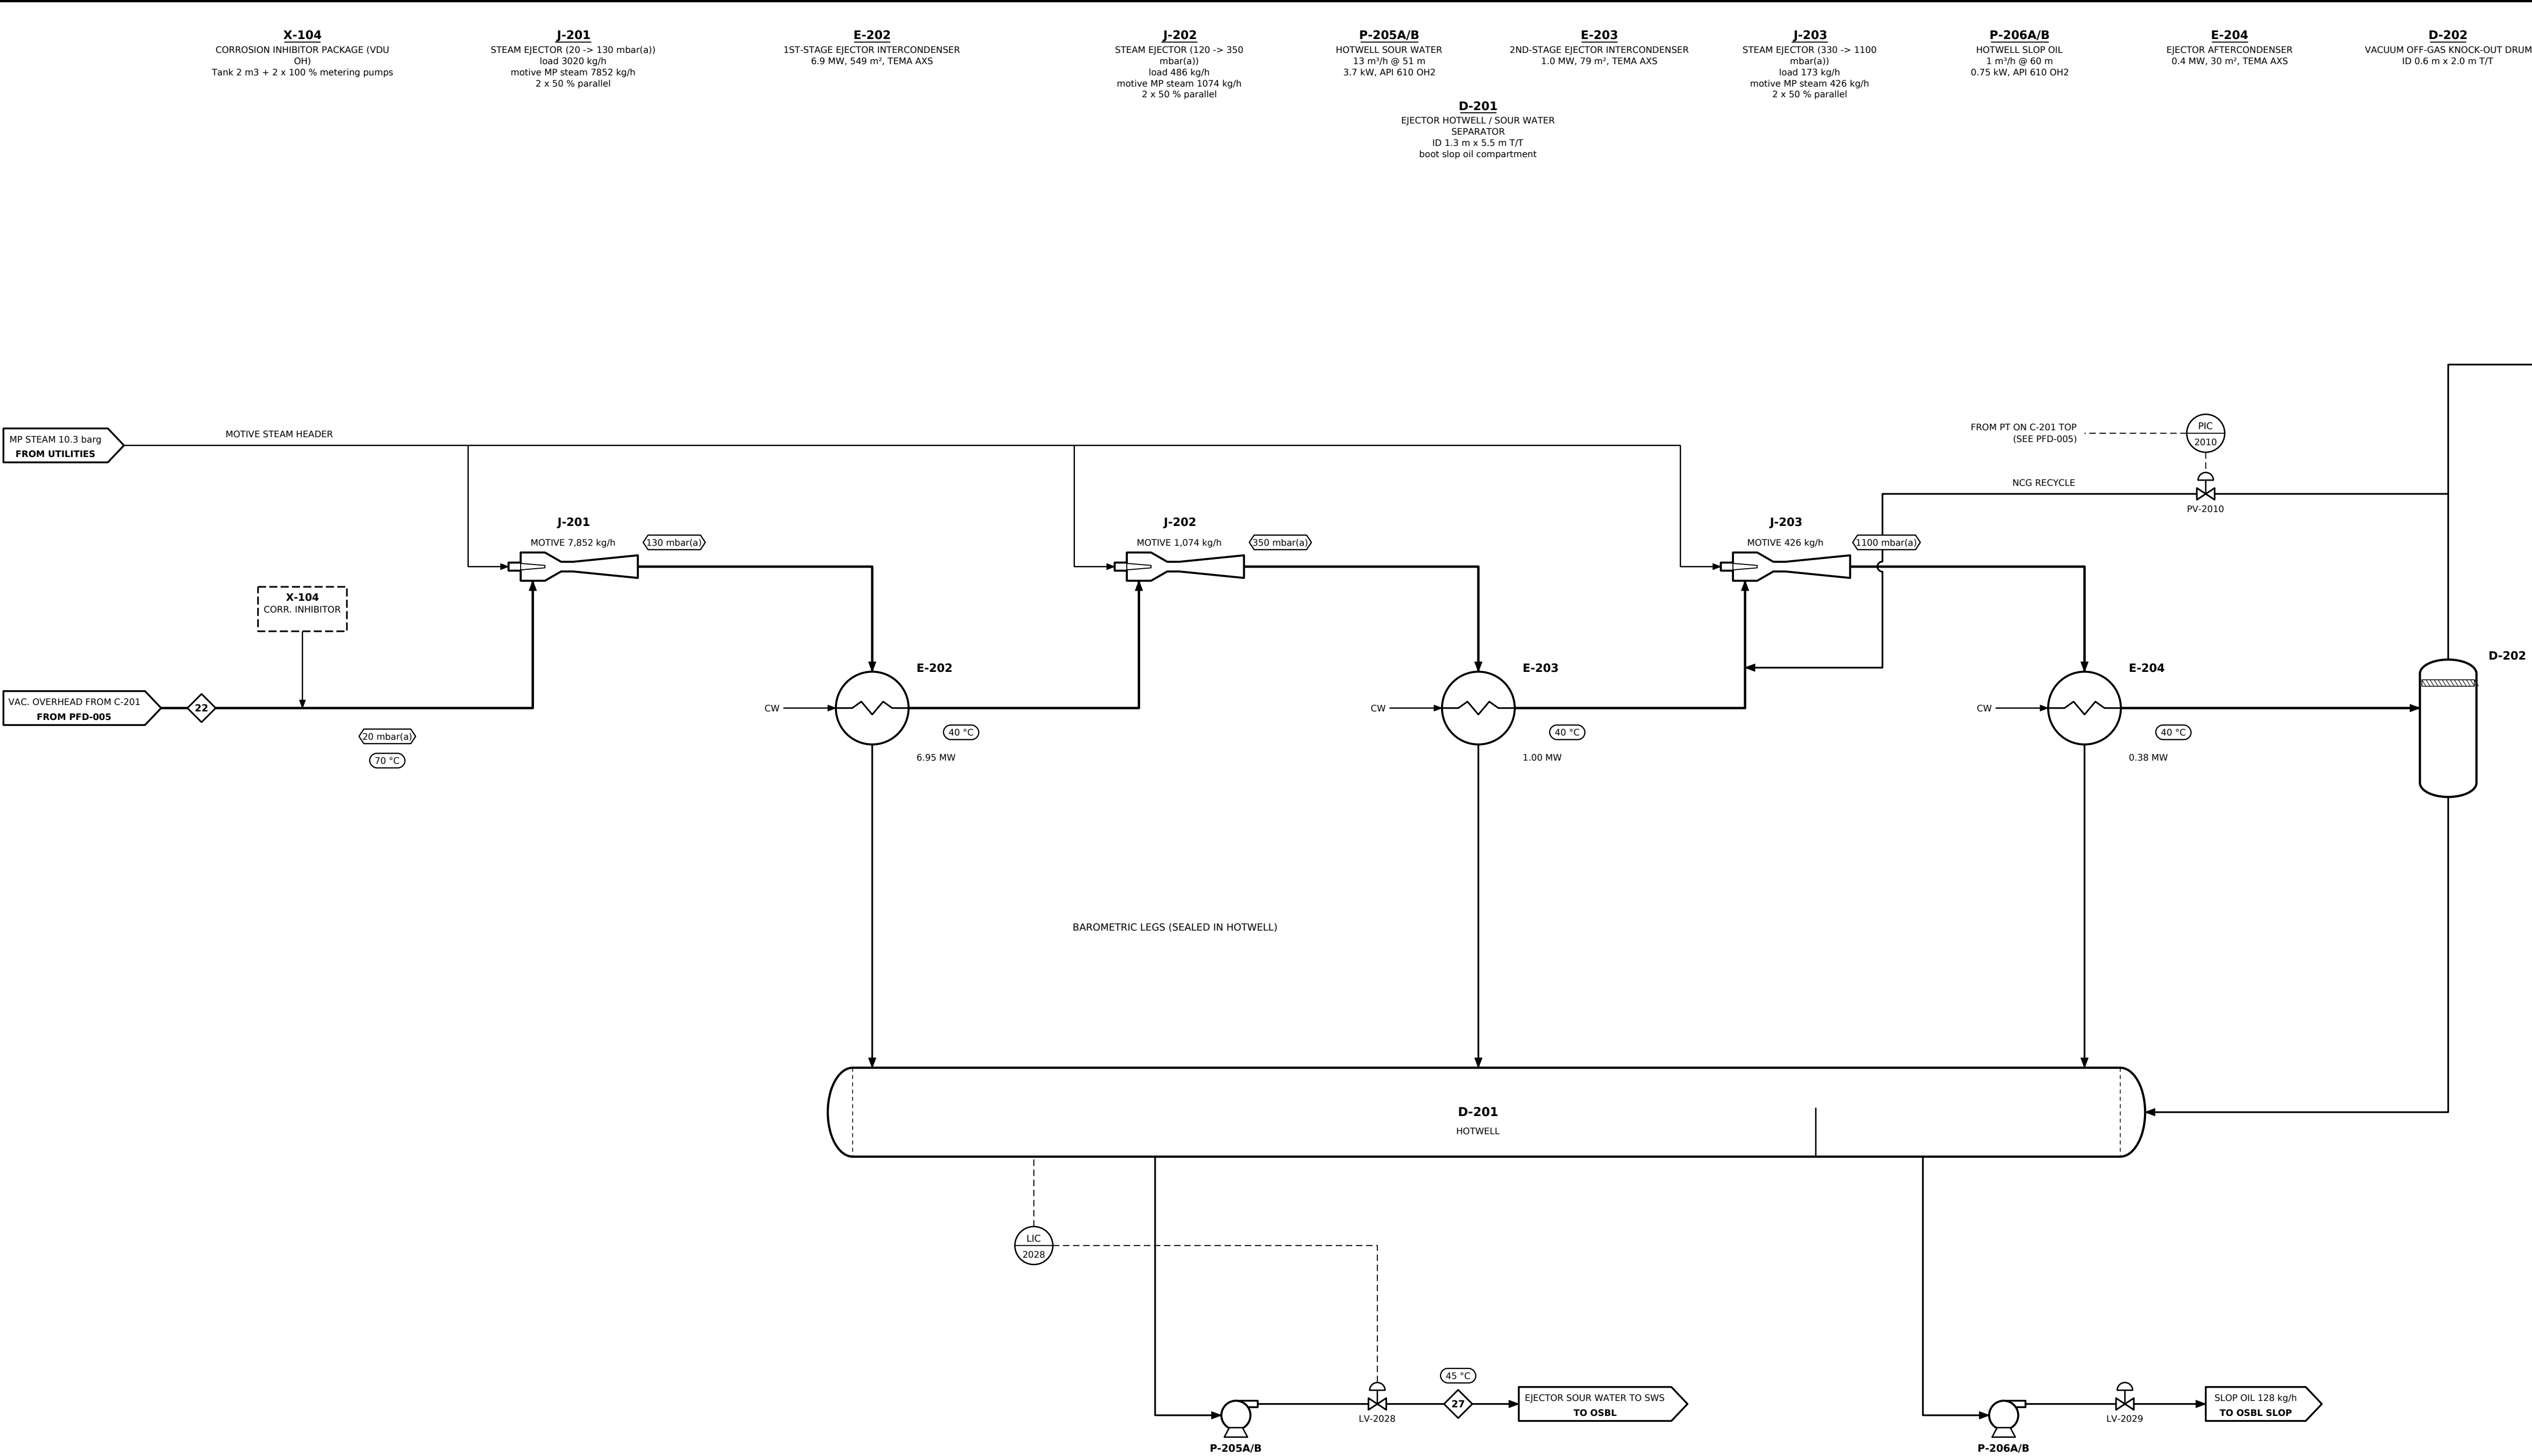

| STREAM No.             | 22                     | 27                 | 28                         |
|------------------------|------------------------|--------------------|----------------------------|
| DESCRIPTION            | Vacuum column overhead | Ejector sour water | Vacuum off-gas (NCG + air) |
| PHASE                  | VAPOUR                 | WATER              | VAPOUR                     |
| TOTAL FLOW kg/h        | 3,020                  | 12,141             | 102                        |
| TEMPERATURE °C         | 70                     | 45                 | 45                         |
| PRESSURE barg          | -0.99                  | 0.5                | 0.0                        |
| STD LIQ. FLOW BPSD     | -                      | -                  | -                          |
| VAPOUR FRACTION (mass) | 1                      | -                  | 1                          |
| MOLECULAR WEIGHT       | -                      | -                  | -                          |

| REV | DATE       | DESCRIPTION              |
|-----|------------|--------------------------|
| A   | 2026-10-02 | Issued for review (FEED) |

GENERIC REFINERY - GULF COAST  
100 KBPSD CRUDE & VACUUM DISTILLATION UNIT

**PROCESS FLOW DIAGRAM**  
VACUUM EJECTOR SYSTEM & HOTWELL

|            |       |       |        |
|------------|-------|-------|--------|
| DISCIPLINE | STAGE | SCALE | SHEET  |
| PROCESS    | FEED  | NTS   | 6 OF 6 |

|             |         |          |            |
|-------------|---------|----------|------------|
| DRAWN       | CHECKED | APPROVED | DATE       |
| CLAUDE CODE | -       | -        | 2026-10-02 |

|                    |     |
|--------------------|-----|
| DRAWING NUMBER     | REV |
| CFU-200-PR-PFD-006 | A   |