

SECTION AT E 96.0 (LOOKING WEST) - SCALE 1:200

Equipment shown: E 70 to section plane E 96; faint = more than 8 m beyond plane

COLUMN NOZZLE ELEVATIONS (FEED, approx.)


C-101			
overhead	EL 143.72	tpa_return	EL 140.45
reflux_return	EL 140.35	tpa_draw	EL 138.23
kero_vapour_return	EL 134.37	mpa_return	EL 133.90
kero_draw	EL 133.81	mpa_draw	EL 131.68
diesel_vapour_return	EL 126.60	bpa_return	EL 126.13
diesel_draw	EL 126.04	tpa_draw	EL 123.93
ago_vapour_return	EL 120.05	ago_draw	EL 119.49
feed	EL 115.61	stripping_steam	EL 110.26
bottoms	EL 104.97		

SIDE STRIPPER NOZZLES

C-102			
vapour_return	EL 113.62	feed	EL 112.30
stripping_steam	EL 104.90	bottoms	EL 103.58

C-103			
vapour_return	EL 113.67	feed	EL 112.30
stripping_steam	EL 104.90	bottoms	EL 103.53

C-104			
vapour_return	EL 113.55	feed	EL 112.30
stripping_steam	EL 104.90	bottoms	EL 103.65

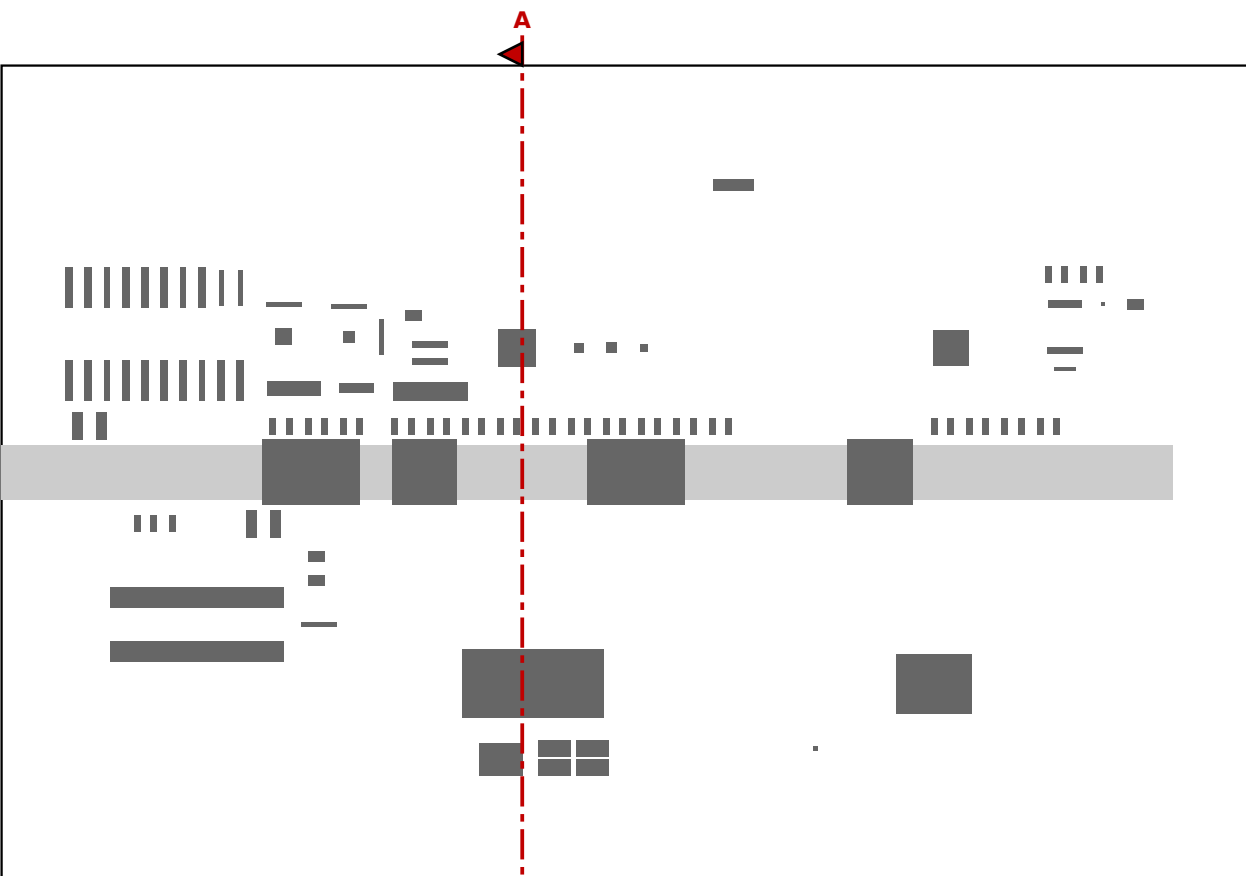

KEY PLAN (NTS) - SECTION PLANE, LOOKING WEST

NOTES

- Elevations in metres: grade (HPP) EL 100.000. Section looking WEST (north to the right).
- Items in front of / at the section plane solid; items beyond shown dashed gray.
- Nozzle elevations approximate (FEED) - from tray spacing 0.61 / 0.76 m per sizing.
- Rack tiers TOS EL 106.0 / 108.5 / 111.0; air coolers on structure above tier 3.
- C-101 skirt height set by P-112 / P-108 NPSH (hot bottoms, 350 C).
- Side strippers C-102/3/4 (east of plane, not shown) fed by gravity from C-101 draws.

REV	DATE	DESCRIPTION	
A	2026-10-02	Issued for review (FEED)	
GENERIC REFINERY - GULF COAST			
100 KBPSD CRUDE & VACUUM DISTILLATION UNIT			
SECTION / ELEVATION			
SECTION N-S THROUGH H-101 / PIPE RACK / C-101 (AREA 100)			
DISCIPLINE	STAGE	SCALE	SHEET
PLANT LAYOUT	FEED	1:200	1 OF 1
DRAWN	CHECKED	APPROVED	DATE
CLAUDE CODE	-	-	2026-10-02
DRAWING NUMBER			REV
CFU-000-PL-ELV-001			A