

D-103


Fuel gas knock-out drum
ID 0.9 m x 2.5 m TTT
DESIGN 7.0 barg / 90 C; CA 3 mm
MAT'L CS

D-104

Flare knock-out drum (unit)
ID 2.1 m x 6.5 m TTT
DESIGN 3.5 barg / 280 C; CA 3 mm
MAT'L CS

P-119A/B

Flare KO drum pump-out
RATED 21 m³/h @ 76 m, dP 6 bar
MOTOR: 7.5 kW; API 682 Plan 11/92
DES. T 90 C; MAT'L S-6 (CS/12Cr)

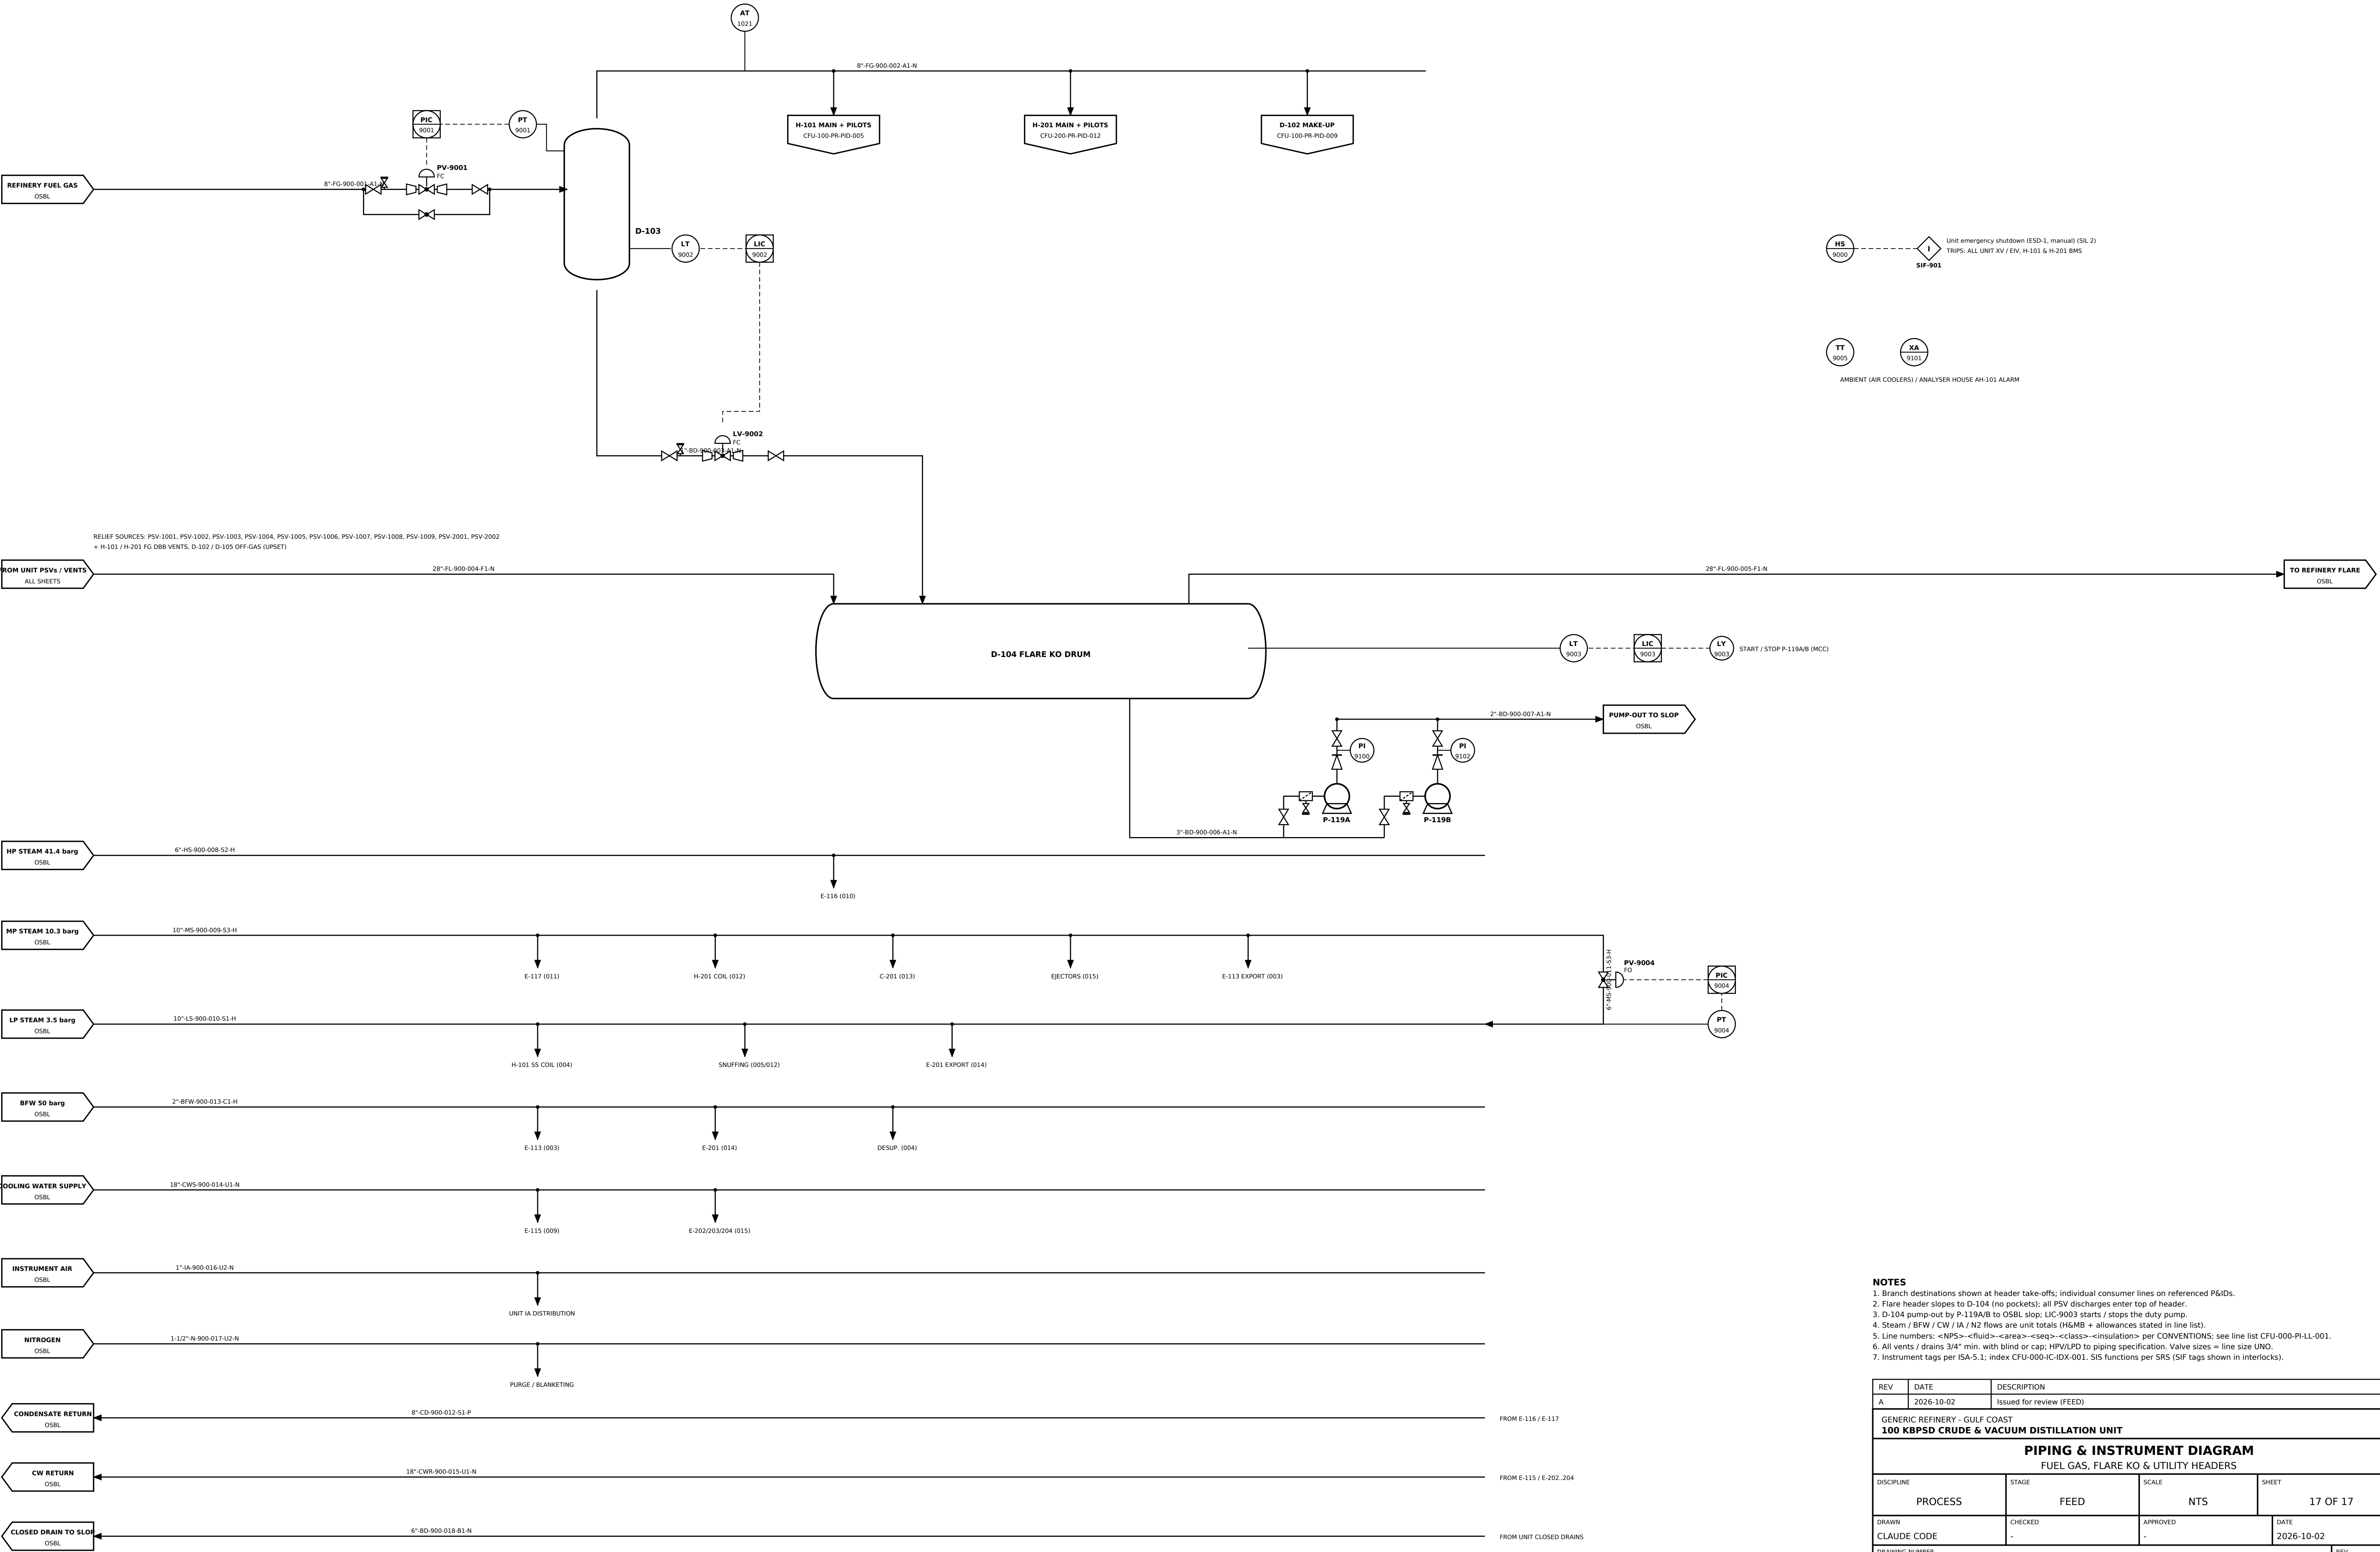

NOTES			
1. Branch destinations shown at header take-offs; individual consumer lines on referenced P&IDs.			
2. Flare header slopes to D-104 (no pockets); all PSV discharges enter top of header.			
3. D-104 pump-out by P-119A/B to OSBL loop; LIC-9003 starts / stops the duty pump.			
4. Steam / BFW / CW / IA / N2 flows are unit totals (HG&B + allowances stated in line list).			
5. Line numbers: <NPS> <fluid> <area> <seg> <class> <insulation> per CONVENTIONS; see line list CFU-000-PI-LL-001.			
6. All vents / drains 3/4" min. with blind or cap; HPV/LD to piping specification. Valve sizes = line size UNDO.			
7. Instrument tags per ISA-5.1; index CFU-000-IC-IDX-001. SIS functions per SRS (SIF tags shown in interlocks).			
REV	DATE	DESCRIPTION	
A	2026-10-02	Issued for review (FEED)	
GENERIC REFINERY - GULF COAST 100 KBPSD CRUDE & VACUUM DISTILLATION UNIT			
PIPING & INSTRUMENT DIAGRAM FUEL GAS, FLARE KO & UTILITY HEADERS			
DISCIPLINE	STAGE	SCALE	SHEET
PROCESS	FEED	NTS	17 OF 17
DRAWN	CHECKED	APPROVED	DATE
CLAUDE CODE	-	-	2026-10-02
DRAWING NUMBER			REV
CFU-000-PR-PID-016			A