


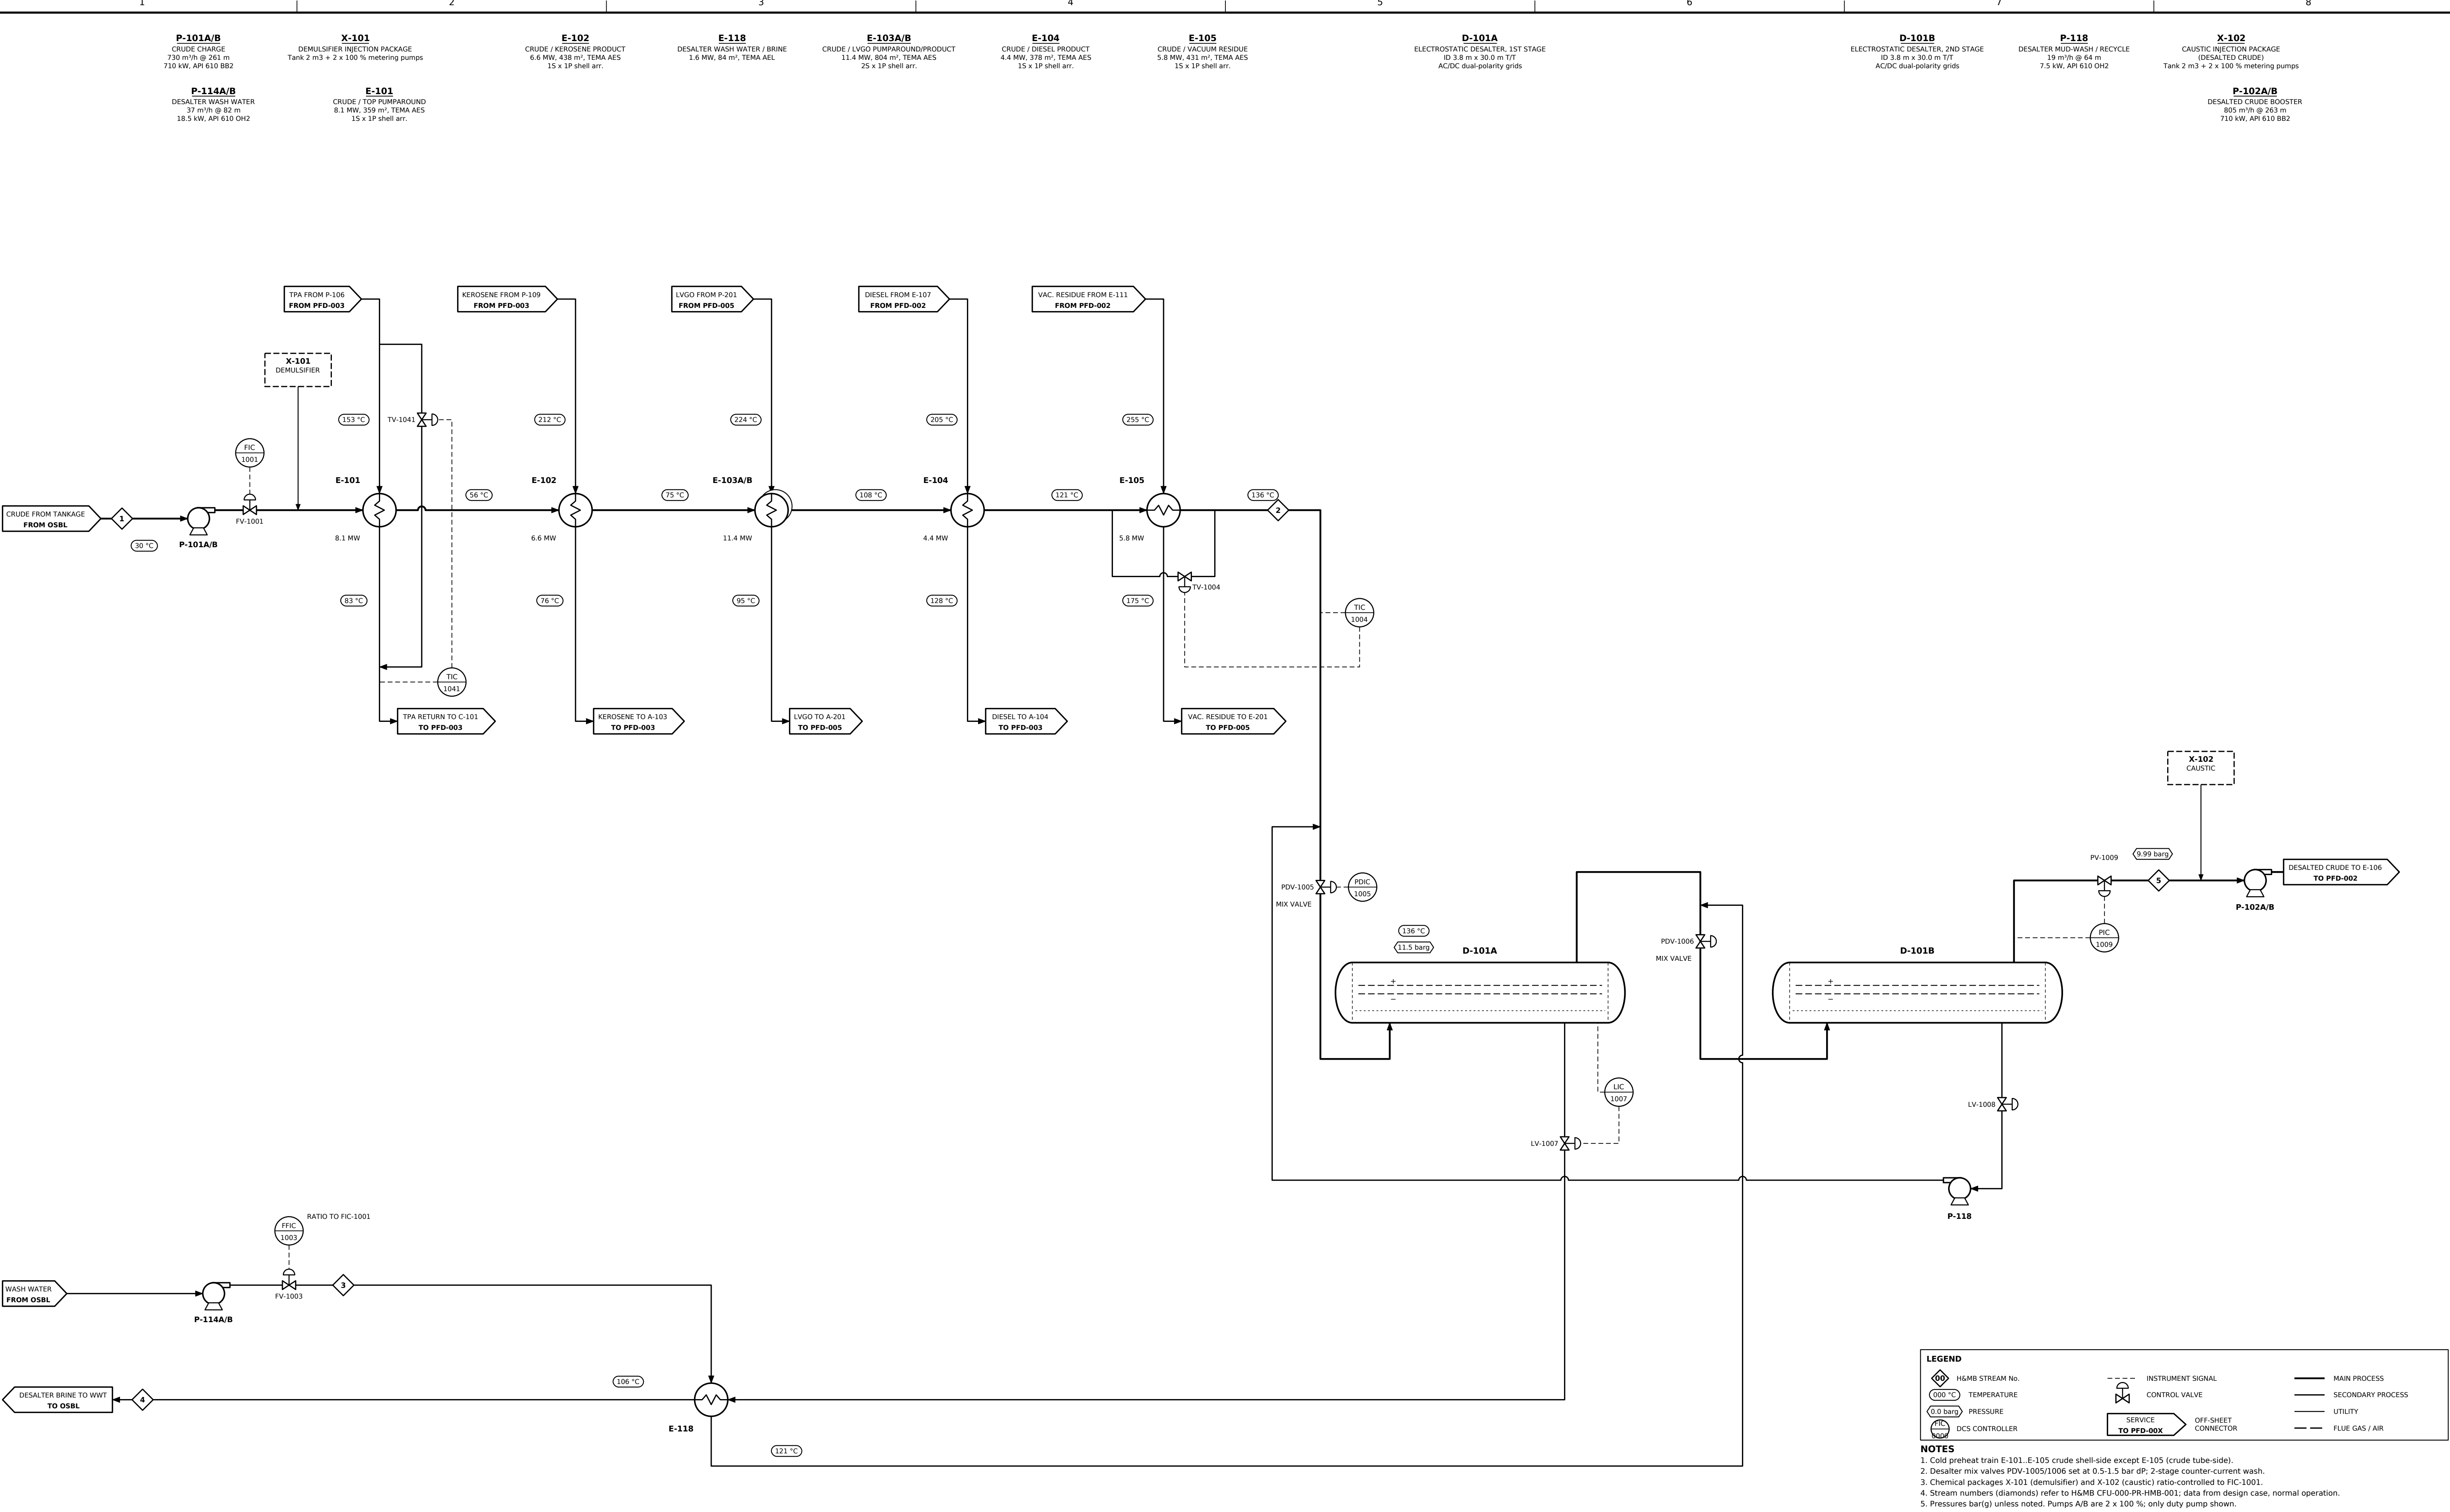

STREAM No.	1	2	3	4	5
DESCRIPTION	Crude from tankage	Crude to desalter	Desalter wash water	Desalter brine	Desalted crude
PHASE	LIQUID	LIQUID	WATER	WATER	LIQUID
TOTAL FLOW kg/h	569,859	569,859	33,089	33,751	569,197
TEMPERATURE °C	30	121	106	106	136
PRESSURE barg	2.0	13.0	15.0	5.0	10.0
STD LIQ. FLOW BPSD	100,000	100,000	-	-	100,000
VAPOUR FRACTION (mass)	0	0	-	-	0
MOLECULAR WEIGHT	215.7	215.7	-	-	215.7

REV	DATE	DESCRIPTION
A	2026-10-02	Issued for review (FEED)
GENERIC REFINERY - GULF COAST		
100 KBPSD CRUDE & VACUUM DISTILLATION UNIT		
PROCESS FLOW DIAGRAM		
CRUDE CHARGE, COLD PREHEAT & DESALTING		
DISCIPLINE	STAGE	SCALE
PROCESS	FEED	NTS
DRAWN	CHECKED	APPROVED
CLAUDE CODE	-	-
DRAWING NUMBER	CFU-100-PR-PFD-001	
DATE	2026-10-02	REV
1 OF 6		A