

SECTION AT E 204.0 (LOOKING WEST) - SCALE 1:200



Equipment shown: E 158 to section plane E 204; faint = more than 40 m beyond plane

COLUMN NOZZLE ELEVATIONS (FEED, approx.)

C-201			
overhead	EL 146.65	lvgo_pa_return	EL 143.37
lvgo_draw	EL 138.52	lvgo_draw	EL 133.97
lvgo_pa_return	EL 133.77	wash_oil_return	EL 127.71
slop_wax_draw	EL 124.18	feed	EL 121.05
stripping_steam	EL 115.76	quench_return	EL 114.56
bottoms	EL 109.25		

C-201 ZONES (EL from / to)

top_head	142.97 - 146.00
bed1_lvgo_pa	140.44 - 142.97
lvgo_collector	137.92 - 140.44
bed1_flash	135.90 - 137.92
lvgo_collector	133.37 - 135.90
bed1_lvgo_pa	129.84 - 133.37
wash_dscr	127.31 - 129.84
bed4_wash	126.10 - 127.31
slop_collector	123.58 - 126.10
flash_zone	118.53 - 123.58
stripping_trays	116.06 - 118.53
sump	110.00 - 116.06

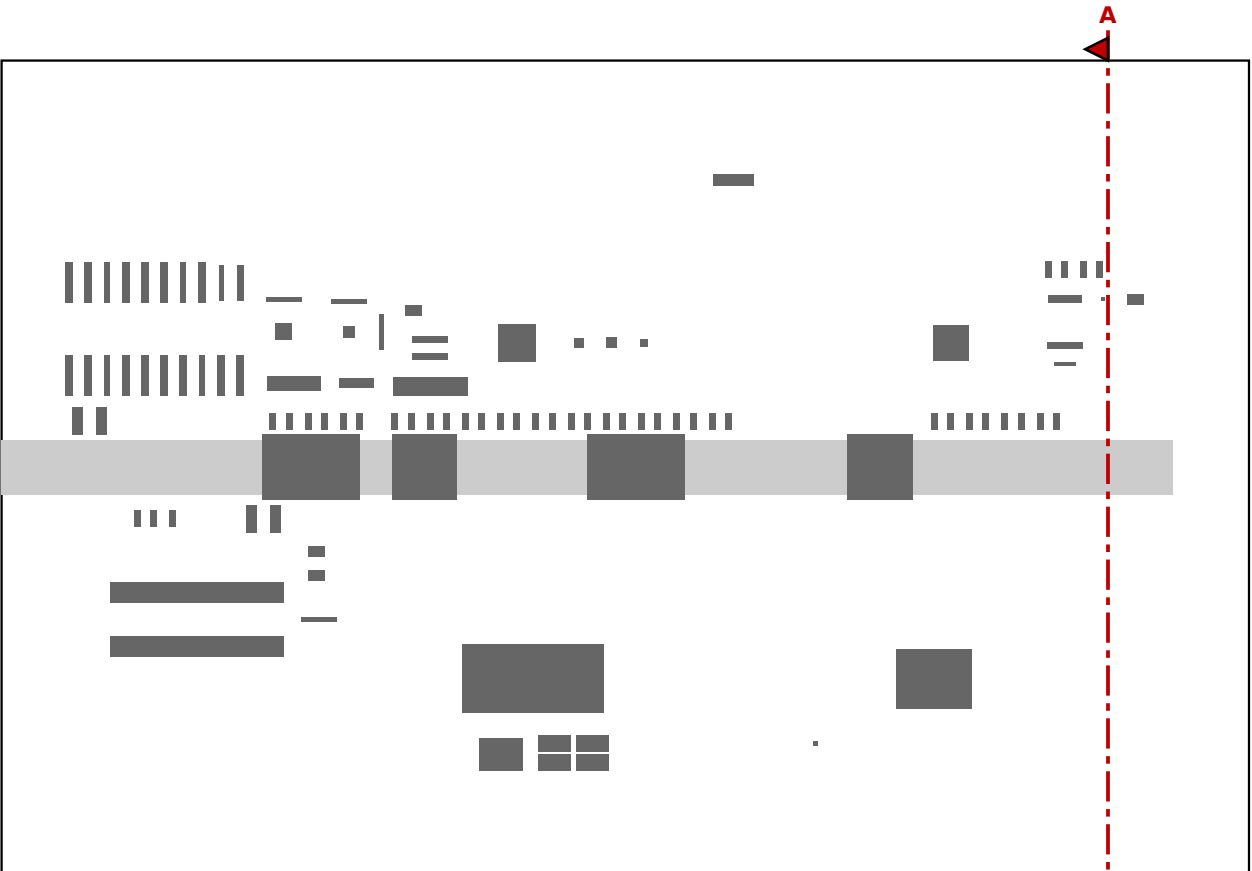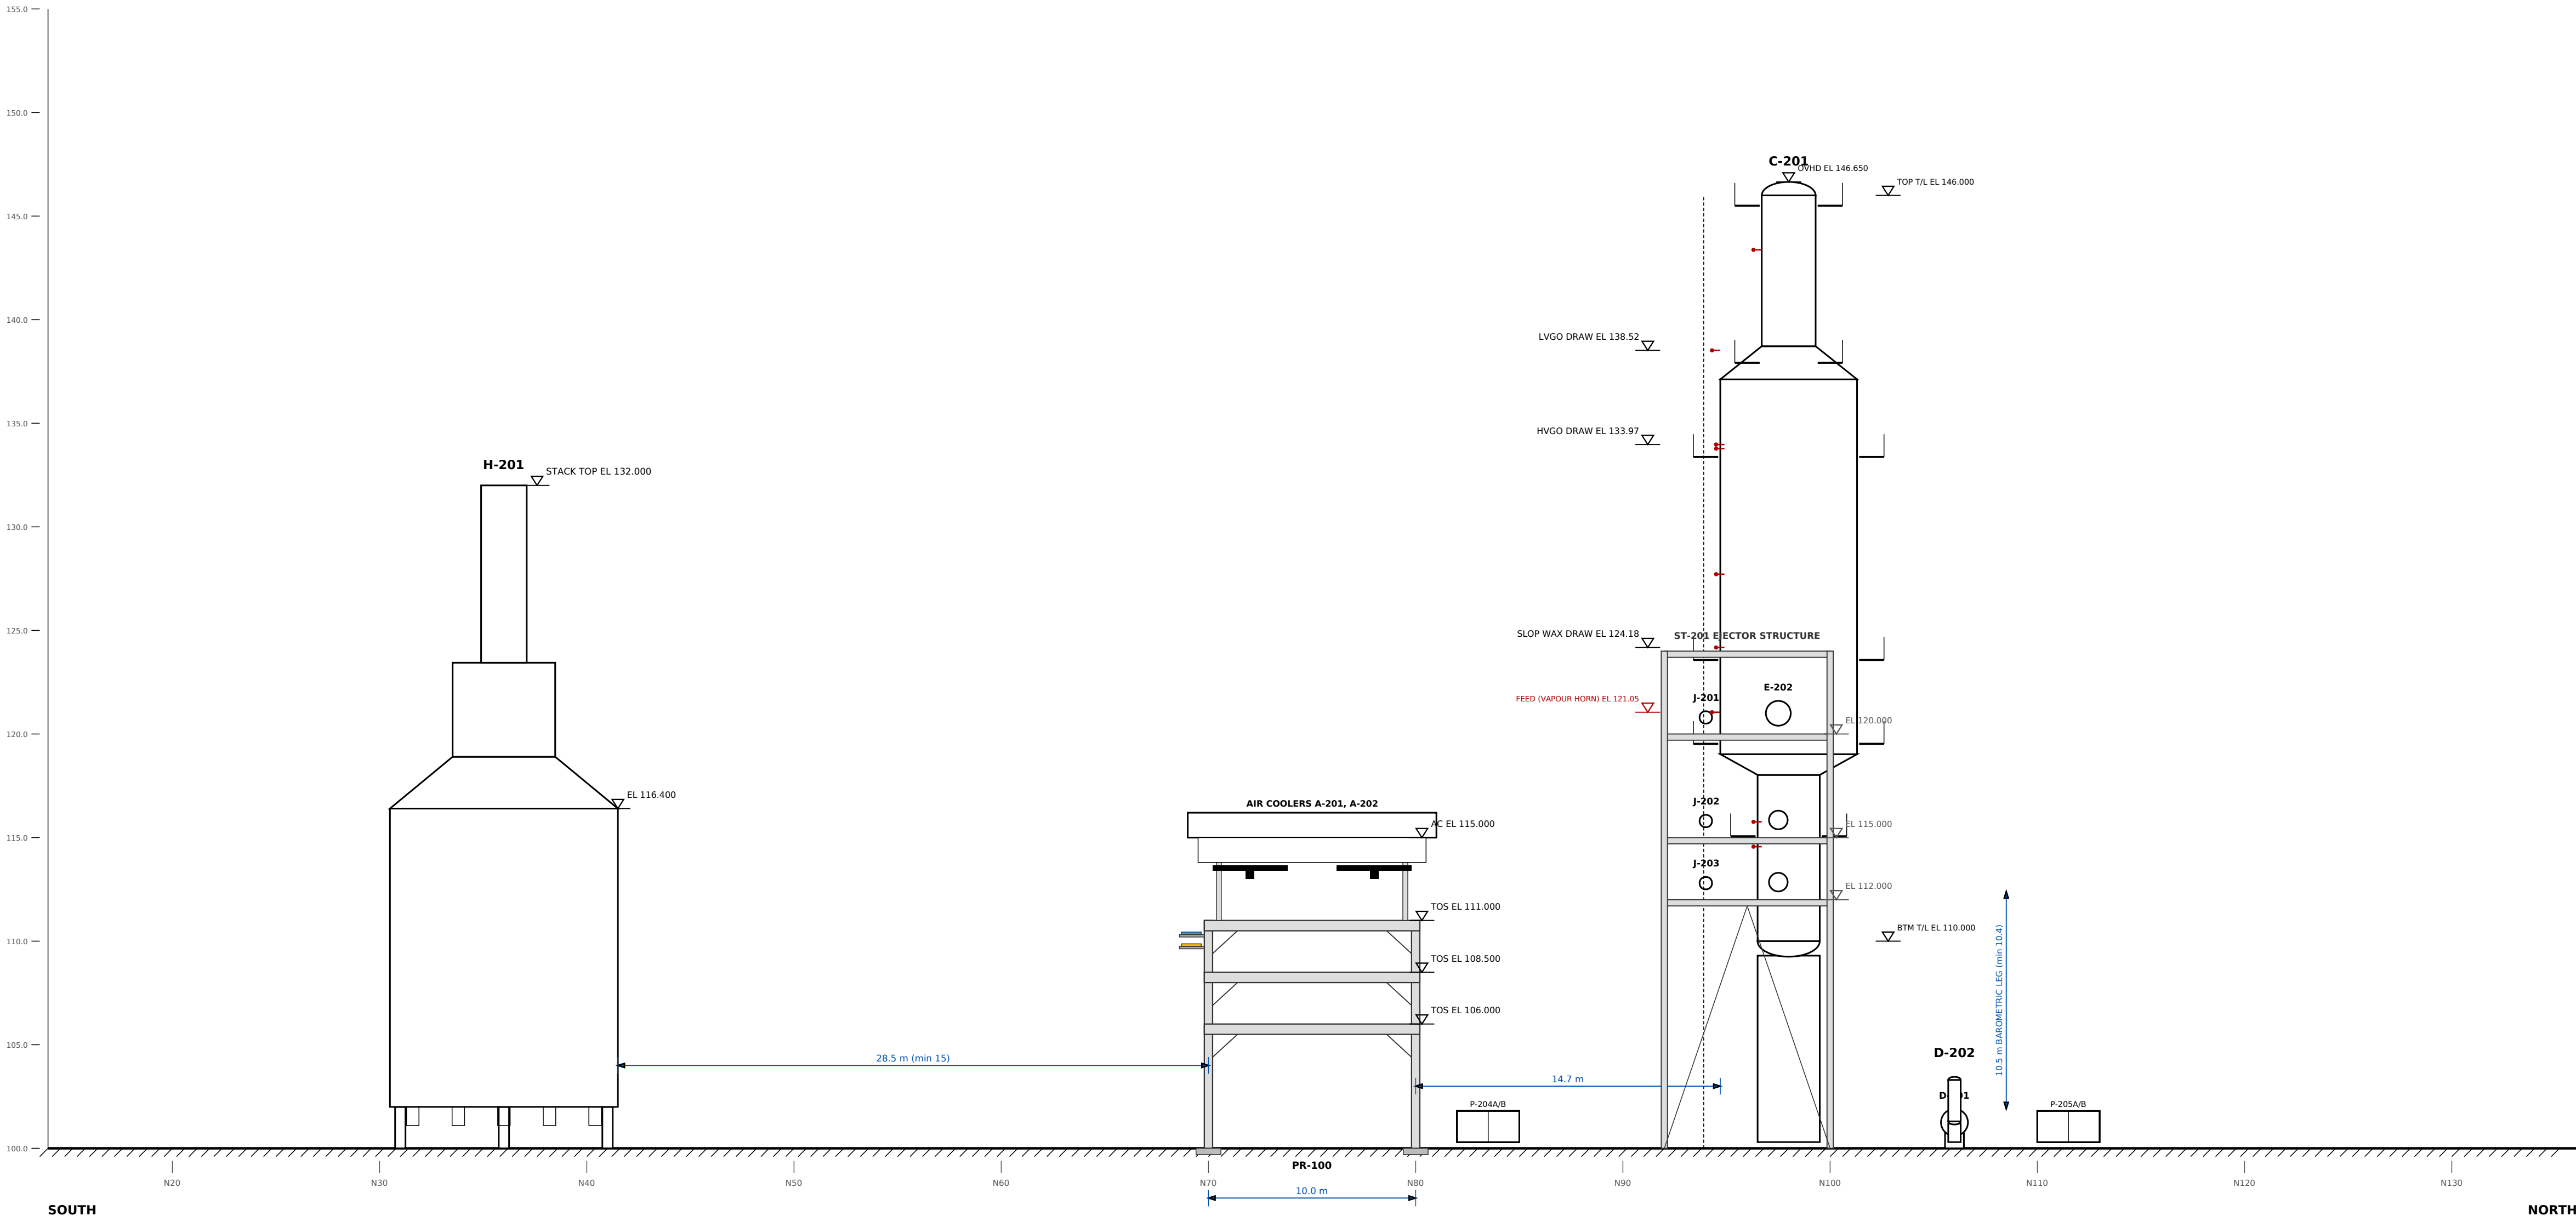

KEY PLAN (NTS) - SECTION PLANE, LOOKING WEST

NOTES

- Elevations in metres: grade (HPP) EL 100.000. Section looking WEST (north to the right).
- Items in front of / at the section plane solid; items beyond shown dashed grey.
- Nozzle elevations approximate (FEED) - from tray spacing 0.61 / 0.76 m per sizing.
- Rack tiers TOS EL 106.0 / 108.5 / 111.0; air coolers on structure above tier 3.
- C-201 bottom T/L EL 110.0 for P-204 NPSH (VR 366 C, quench).
- Ejector condensers on ST-201 >= 10.4 m above hotwell D-201 (barometric legs).

REV	DATE	DESCRIPTION	
A	2026-10-02	Issued for review (FEED)	
GENERIC REFINERY - GULF COAST			
100 KBPSD CRUDE & VACUUM DISTILLATION UNIT			
SECTION / ELEVATION			
SECTION N-S THROUGH H-201 / PIPE RACK / C-201 (AREA 200)			
DISCIPLINE	STAGE	SCALE	SHEET
PLANT LAYOUT	FEED	1:200	1 OF 1
DRAWN	CHECKED	APPROVED	DATE
CLAUDE CODE	-	-	2026-10-02
DRAWING NUMBER			REV
CFU-000-PL-ELV-002			A