


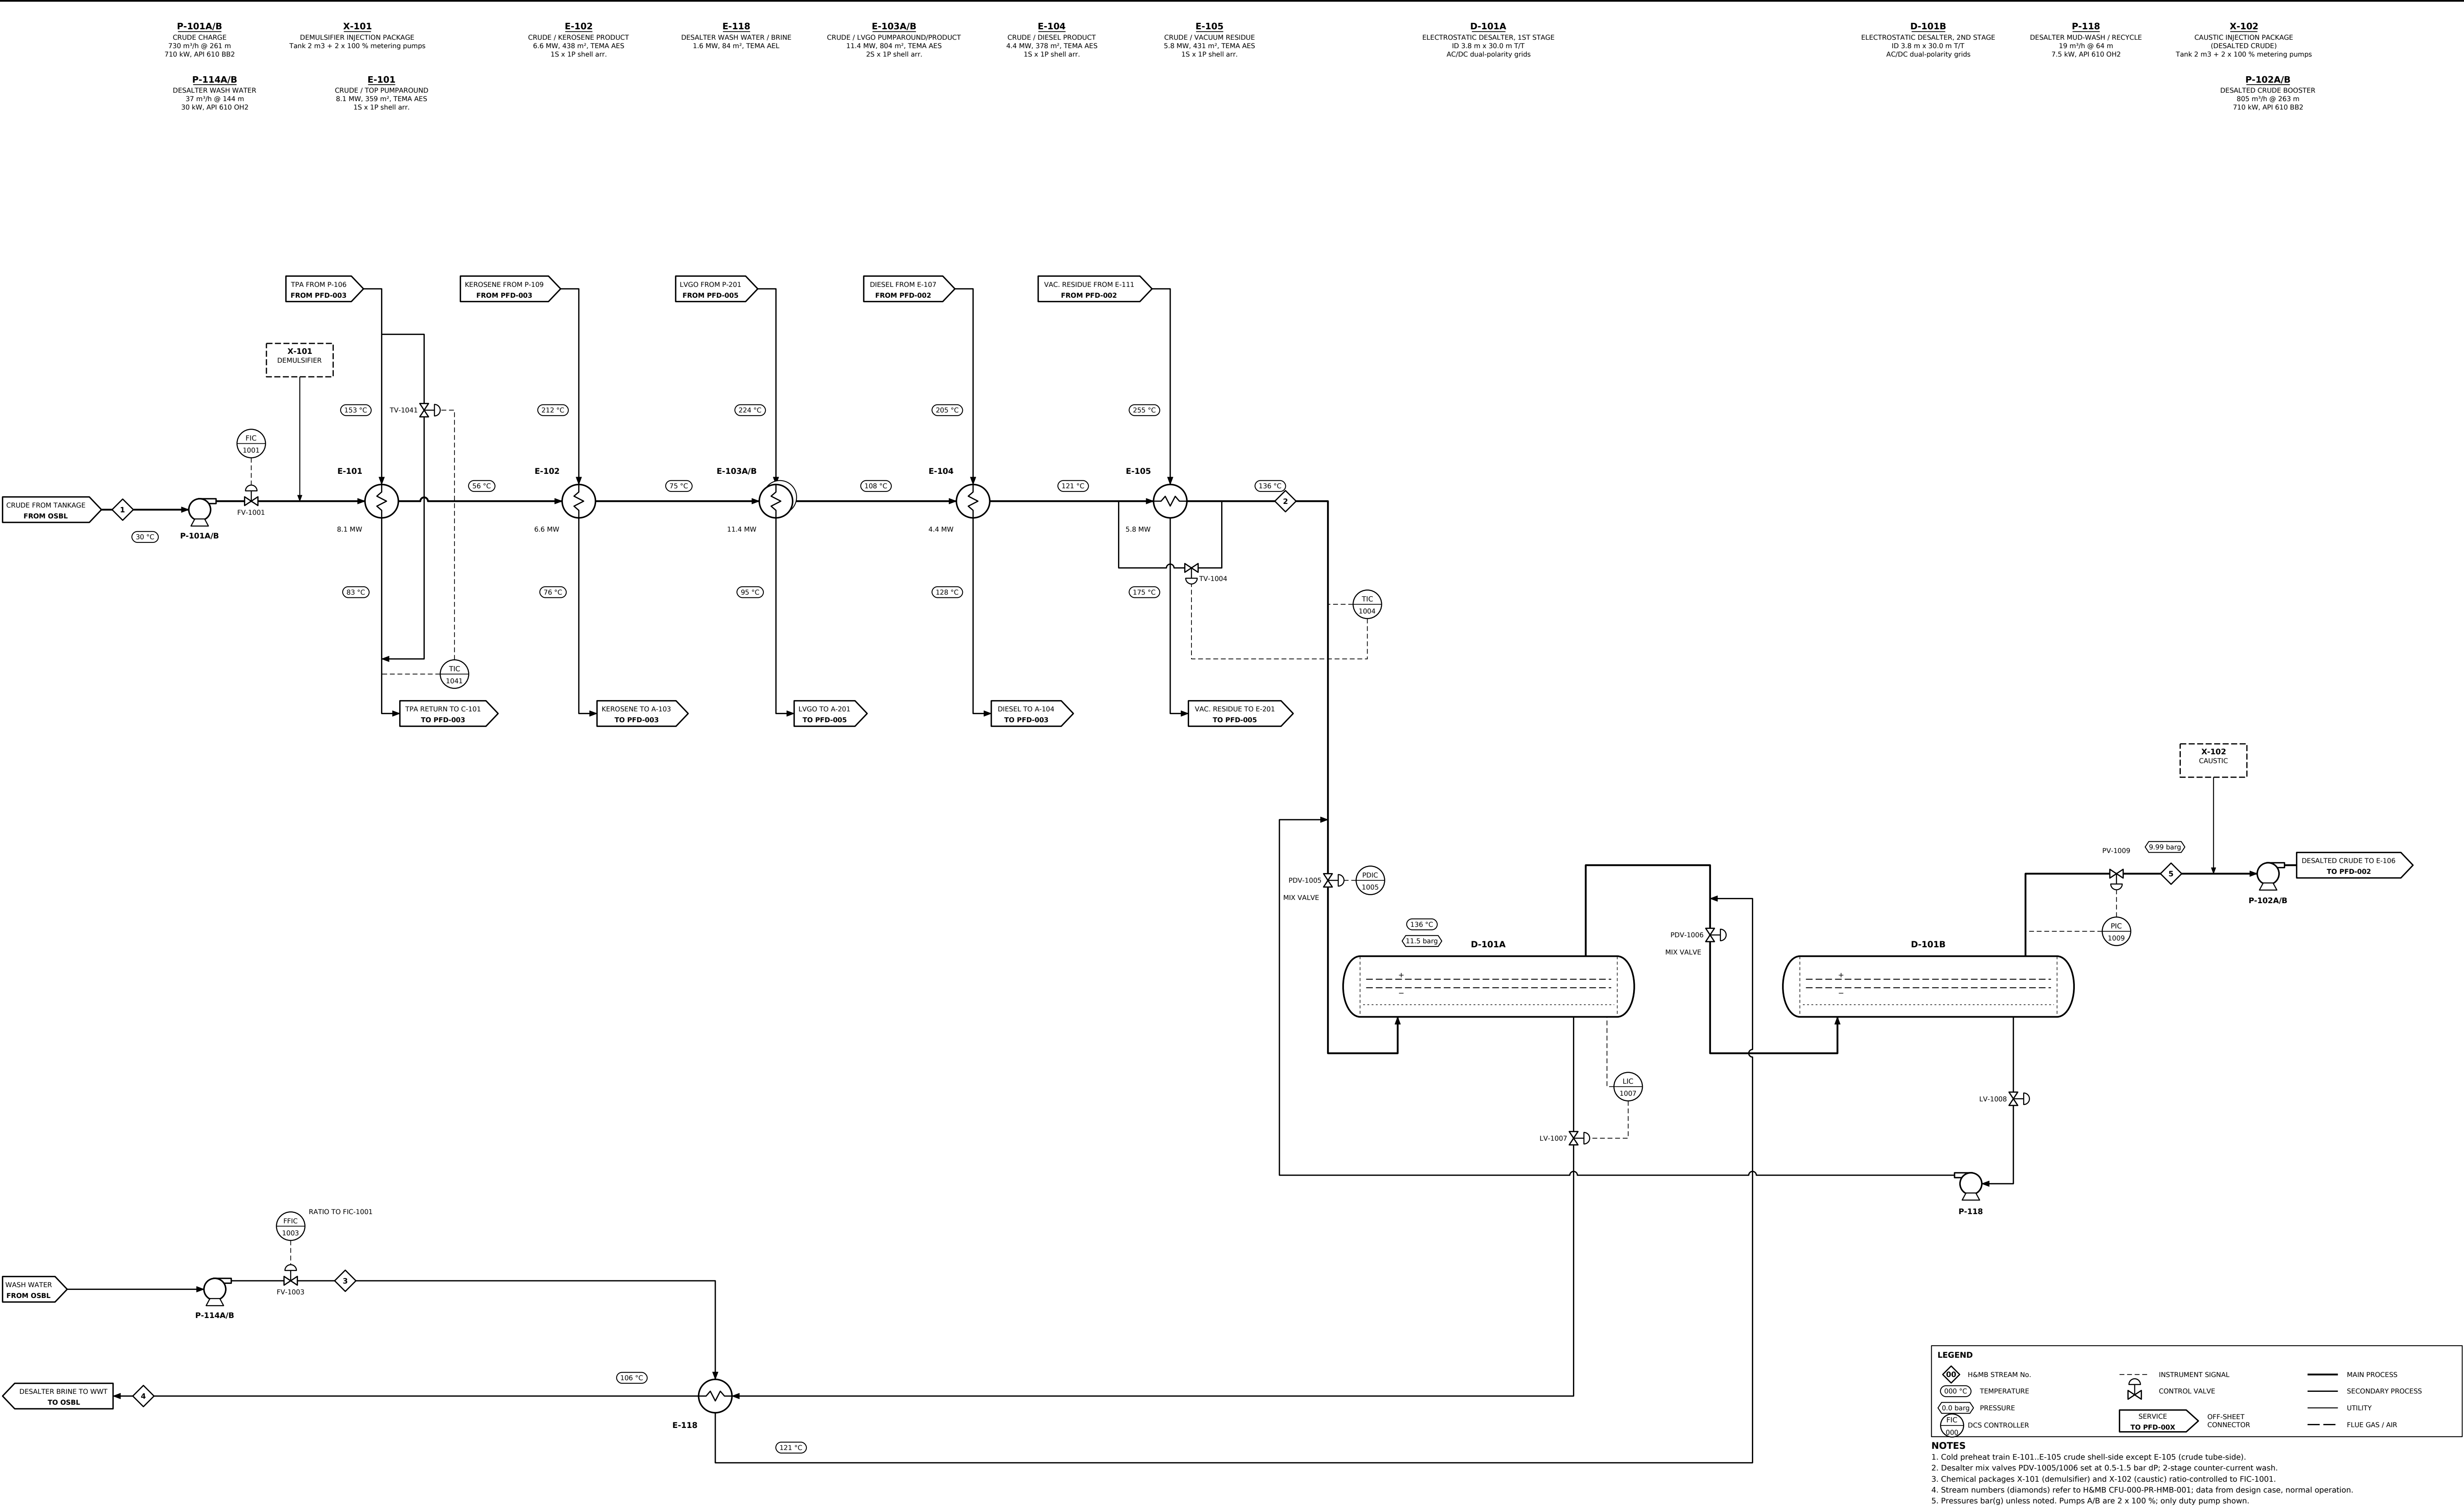

STREAM No.	1	2	3	4	5
DESCRIPTION	Crude from tankage	Crude to desalter	Desalter wash water	Desalter brine	Desalted crude
PHASE	LIQUID	LIQUID	WATER	WATER	LIQUID
TOTAL FLOW kg/h	569,859	569,859	33,089	33,751	569,197
TEMPERATURE °C	30	121	106	106	136
PRESSURE barg	2.0	13.0	15.0	5.0	10.0
STD LIQ. FLOW BPSD	100,000	100,000	-	-	100,000
VAPOUR FRACTION (mass)	0	0	-	-	0
MOLECULAR WEIGHT	215.7	215.7	-	-	215.7

H&MB STREAM No.

TEMPERATURE

PRESSURE

DCS CONTROLLER

INSTRUMENT SIGNAL

CONTROL VALVE

SERVICE TO PFD-00X

MAIN PROCESS

SECONDARY PROCESS

UTILITY

FLUE GAS / AIR

NOTES

1. Cold preheat train E-101, E-105 crude shell-side except E-105 (crude tube-side).

2. Desalter mix valves PDV-1005/1006 set at 0.5-1.5 bar dPi; 2-stage counter-current wash.

3. Chemical packages X-101 (demulsifier) and X-102 (caustic) ratio-controlled to FIC-1001.

4. Stream numbers (diamonds) refer to H&MB CFU-000-PR-HMB-001; data from design case, normal operation.

5. Pressures bar(g) unless noted. Pumps A/B are 2 x 100 %; only duty pump shown.

REV	DATE	DESCRIPTION	
A	2026-10-02	Issued for review (FEED)	
GENERIC REFINERY - GULF COAST			
100 KBPSD CRUDE & VACUUM DISTILLATION UNIT			
PROCESS FLOW DIAGRAM			
CRUDE CHARGE, COLD PREHEAT & DESALTING			
DISCIPLINE		STAGE	SCALE
PROCESS		FEED	NTS
		SHEET	
		1 OF 6	
DRAWN	CHECKED	APPROVED	DATE
CLAUDE CODE	-	-	2026-10-02
DRAWING NUMBER			REV
CFU-100-PR-PFD-001			A